



WINCHESTER RD.

AREA OF WORK

HACK'S CROSS RD.

0 20' 40' 80'

1" = 40'-0"

TSG-1	TITLE SHEET
C1-0	COVER
C2-0	SURVEY
C3-0	SITE DEMOLITION PLAN
C4-0	OVERALL LAYOUT PLAN
C4-1	SITE LAYOUT PLAN
C5-0	DETAILED UTILITY PLAN
C6-0	DETAILED GRADING PLAN
C6-1	DETAILED GRADING PLAN
C6-2	PROFILES
C7-0	INITIAL EROSION CONTROL PLAN
C7-1	INTERMEDIATE AND FINAL EROSION CONTROL PLAN
D1-0	CONSTRUCTION DETAILS
D1-1	CONSTRUCTION DETAILS S
D1-2	CONSTRUCTION DETAILS
L1-0	TREE REPLACEMENT PLAN I
L1-1	TREE REPLACEMENT PLAN II
SE-1	SITE ELECTRICAL
DA-0-1	DEMOLITION SITE PLAN
AG-1	ENLARGED SITE PLAN
AG-2	CANOPY ELEVATIONS AND SECTIONS
AG-4	CANOPY REFLECTED CEILING PLAN
AG-5	CONTROLLER ENCLOSURE PLANS, ELEVATIONS AND DETAILS
S1-0	SITE ELECTRICAL
S1-0	CANOPY SPECIAL INSPECTIONS AND GENERAL NOTES
S1-1	CANOPY FOUNDATION PLAN
S1-2	CANOPY FOUNDATION DETAILS
S2-0	CANOPY ROOF FRAMING PLAN
S2-1	CANOPY ROOF FRAMING DETAILS

OWNER

COSTCO WHOLESALE CORPORATION
730 LAKE DRIVE
ISSAQUAH, WA 98027
T: 425.313.8100

ARCHITECT

MG2 CORPORATION
8444 WESTPARK DRIVE, SUITE 120
MAGLEEN, WA 22102
T: 703.564.8406
T: 703.564.8400
PROJECT MANAGER: AGNES VINCENT

**CIVIL ENGINEER
AND SURVEYOR**

AEC
50 WARM SPRINGS CIRCLE
SUITE 110
ROSWELL, GA 30075
T: 678.990.2408

**GEOTECHNICAL
ENGINEER**

TERRACON CONSULTANTS, INC.
4040 ROYAL DRIVE, SUITE 100
KENNESAW, GA 30144
T: 770.623.0755

**LANDSCAPE
ARCHITECT**

AEC
50 WARM SPRINGS CIRCLE
SUITE 110
ROSWELL, GA 30075
T: 678.990.2408

**STRUCTURAL
ENGINEER**

GMA
301 N. FIRST ST., SUITE 110
FRESNO, CA 93720
T: 559.435.1411
T: 559.435.1189

**TANK/
ELECTRICAL/
ENGINEER**


BARGHAUSEN CONSULTING ENGINEERS, INC.
18215 JENNY AVENUE SOUTH
KENT, WA 98032
T: 425.251.8222
T: 425.251.8782

GOVERNING BUILDING CODE:	2021 INTERNATIONAL BUILDING CODE W/ LOCAL AMENDMENTS 2021 INTERNATIONAL MECHANICAL CODE W/ LOCAL AMENDMENTS 2021 FUEL GAS CODE W/ LOCAL AMENDMENTS 2020 NATIONAL ELECTRIC CODE W/ TENN. AMENDMENTS 2021 INTERNATIONAL PLUMBING CODE W/ LOCAL AMENDMENTS 2021 INTERNATIONAL ENERGY CONSERVATION CODE W/ LOCAL AMENDMENTS
OCCUPANCY GROUP:	M
CONSTRUCTION TYPE:	II B (NOT RATED)
FUEL CANOPY AREA:	4.575 SQ FT
FUEL CANOPY HEIGHT:	17'-0" TO TOP OF CANOPY


FOR ADDITIONAL ABBREVIATIONS:
SEE OTHER DESIGN DISCIPLINES

ADJ	ADJUSTABLE, ADJACENT	E	EXISTING	MTL	METAL	REQD	REQUIRED
ALUM	ALUMINUM	ENCL	ENCLOSURE	MFG	MANUFACTURING	SCHED	SCHEDULE
APPROX	APPROXIMATE	EQ	EQUAL	MFR	MANUFACTURER	SHT	SHEET
BD	BOARD	ETC	ET CETERA	MH	MANHOLE	SIM	SIMILAR
BLDG	BUILDING	EXH	EXHAUST	MIN	MINIMUM	SIO	SUPPLIED & INSTALLED BY OWNER
BLK	BLOCK	EXIST	EXISTING	MISC	MISCELLANEOUS	SIV	SUPPLIED & INSTALLED BY VENDOR
BKG	BLOCKING	EXP	EXPANSION	MTR	MOUNTING RESISTANT	SAW-CUT	SAW-CUT
BM	BEAM	EXT	EXTENDING	MTD	MOUNTED	SOIC	SUPPLIED BY OWNER & INSTALLED BY CONTRACTOR
BTWN	BETWEEN	FD	FLOOR DRAIN	MTS	MOUNTINGS	SPEC'D	SPECIFIED
CB	CATCH BASIN	FF	FINISHED FLOOR	NIC	NOT IN CONTRACT	SQ	SQUARE
CI	CAST IRON	FL	FLOOR	NOM	NOMINAL	SS	SANITARY SEWER
CJ	COST IN PLACE	FIN	FINISH	NOT	NOT TO SCALE	STD	STANDARD
CJ	CONSTRUCTION JOINT	FT	FEET	OA	OVERALL	STL	STEEL
CL	CENTER LINE	FTG	FOOTING	OC	ON CENTER	STRUCT	STRUCTURE, STRUCTURAL
CLR	CLEAR	GA	GAUGE	OH	OVERHEAD	SYS	SYSTEM
CMU	CONCRETE MASONRY UNIT	GC	GENERAL CONTRACTOR	OPER	OPERATION	T & E	TANK & ELECTRICAL
COL	COLUMN	HC	HANDICAPPED	OPG	OPENING	TOP	TOP OF MASONRY
CONC	CONCRETE	HORIZ	HORIZONTAL	OPP	OPPOSITE	TOS	TOP OF STORY
CONT	CONTINUOUS	HT	HEIGHT	PVC	POLY VINYL CHLORIDE	TS	TUBE STEEL
CONSTR	CONSTRUCTION	HTR	HEATER	PL	PLATE, PROPERTY LINE	TYL	TYPE
CORP	CORPORATION	IBC	INTERNATIONAL BLDG CODE	PROJ	PROJECT	UNITED	UNITED LABORATORIES
DBL	DOUBLE	INSUL	INSULATION	PRV	PRESSURE REDUCING VALVE	UTIL	UTILITY
DIA	DIAMETER	INT	INTERIOR	PT	POINT	UNL	UNLESS NOTED OTHERWISE
DIM	DIMENSION	JTS	JOINT JOISTS	QTR	QUARTER	UNCH	UNCHANGED
DLS	DETAIL	LCD	LIQUID CRYSTAL DISPLAY	R	RADIUS	VERT	VERTICAL
DOWNSP	DOWNSPOUT	LF	LINEAR FOOT, LINEAL FOOT	RCP	REFLECTED CEILING PLAN	VIF	VERIFY IN FIELD
DWG	DRAWING	LQ	LIQUID	RD	ROOF DRAIN	WAREHOUSE	WAREHOUSE
EA	EACH	MAS	MASONRY	RF	ROOF FORMED	W	WIDTH
ELEC	ELECTRICAL	MAX	MAXIMUM	RL	RAIN LEADER	W	WITH
ELEV	ELEVATION	MBS	METAL BUILDING SYSTEM	REC'D	RECEIVED	W/O	WITHOUT
		MECH	MECHANICAL	REINF	REINFORCING	WDW	WINDOW
						WP	WATERPROOF
						WR	WATER RESISTANT


SYMBOLS

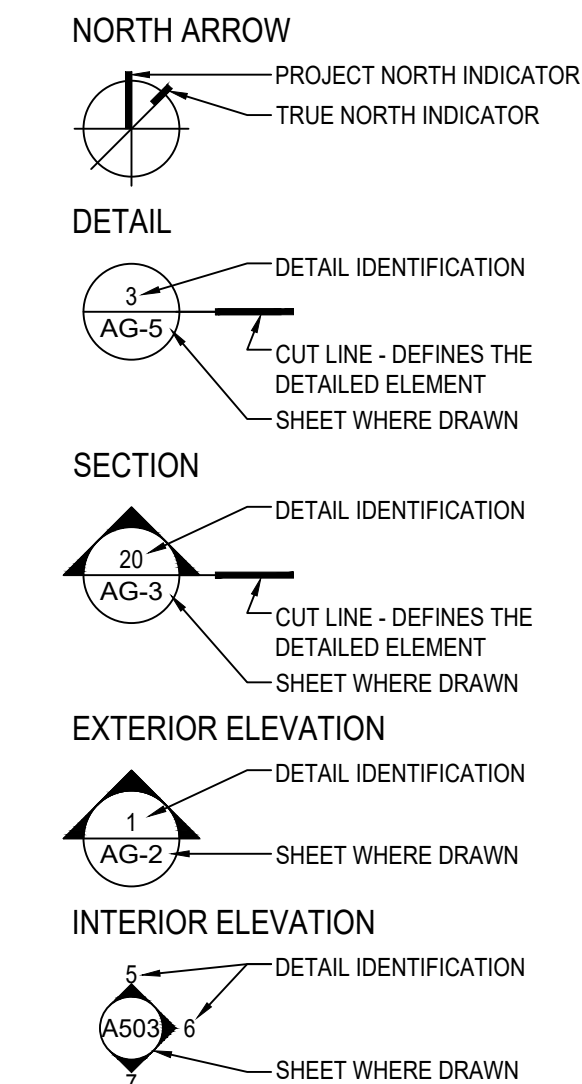

EQUIPMENT MARK

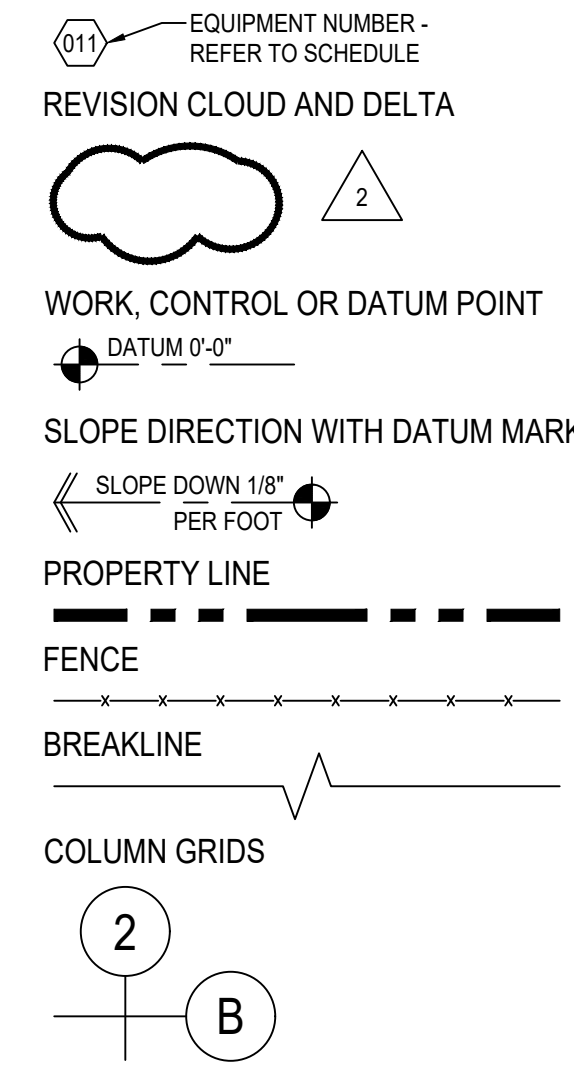

MATERIALS

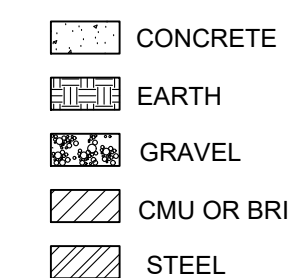

THE FOLLOWING DESCRIBED REAL PROPERTY IS SITUATED IN THE CITY OF S.E. MEMPHIS,
SHELBY COUNTY, STATE OF TENNESSEE.

1. ZONING:	PLANNED DEVELOPMENT
2. SETBACKS:	REQUIRED
FRONT:	24 FT
REAR:	NONE
SIDE:	20 FT
3. SITE AREA:	14.24 ACRES (820,460 S.F.)
4. LOT COVERAGE ALLOWED:	100%
5. LANDSCAPING REQUIRED:	YES, SEE CIVIL
6. EXISTING BUILDING AREA:	
BUILDING FOOTPRINT AREA:	149.48 SQ FT
7. PARKING REQUIRED:	
1/300 SQ FT x 149.448 SQ FT TOTAL = 498 PARKING SPACES REQ'D	
8. PARKING PROVIDED:	
EXISTING PARKING:	709 STALLS
DELETED PARKING:	36 STALLS
TOTAL:	683 STALLS
PARKING RATIO:	683 STALLS (15 ACCESSIBLE STALLS) 1/300 SQ FT

FUELING FACILITY EXPANSION:

THE SCOPE OF WORK INCLUDES ADDING THREE (3) NEW ISLANDS WITH ONE DOUBLE SIDED FUEL DISPENSER EACH; ALLOWING FOR SIX (6) ADDITIONAL AUTOMOBILE FUELING POSITIONS, REMOVING AND REPLACING THE EXISTING (6) DISPENSERS, ENLARGING THE EXISTING CANOPY BY 1,696 SQUARE FEET, AND CURBS, CONCRETE, ASPHALT AND LANDSCAPE REVISIONS. THE EXISTING CONTROLLER ENCLOSURE WILL BE DEMOLISHED AND A NEW ONE WILL BE PROVIDED.

THE NINE (9) NEW DISPENSERS WILL BE INTEGRATED INTO THE COMPUTERIZED CONTROLLER, WHICH RUNS THE PAYMENT, PUMPING AND MONITORING SYSTEMS. FUEL IS STORED IN THREE (3) EXISTING DOUBLE WALLED, FIBERGLASS UNDERGROUND STORAGE TANKS.

THE NEW CONTROL / MONITORING SYSTEM WILL INCLUDE AN ALARM TIED INTO THE OWNER'S CONTRACTED 24 HOUR MONITORING SERVICE COMPANY. THE CONTINUOUS LEAK DETECTION SYSTEM WILL AUTOMATICALLY CHECK FOR FUEL LEAKS AND AUTOMATICALLY WILL STOP THE FLOW OF GASOLINE IN THE EVENT OF AN ALARM CONDITION.

[illegible]


98-4150-19
RM: AGNES VINCENT

RAWN: AV
AUGUST 08, 2023

AUGUST 08, 2023

TITLE SHEET

TSG-1

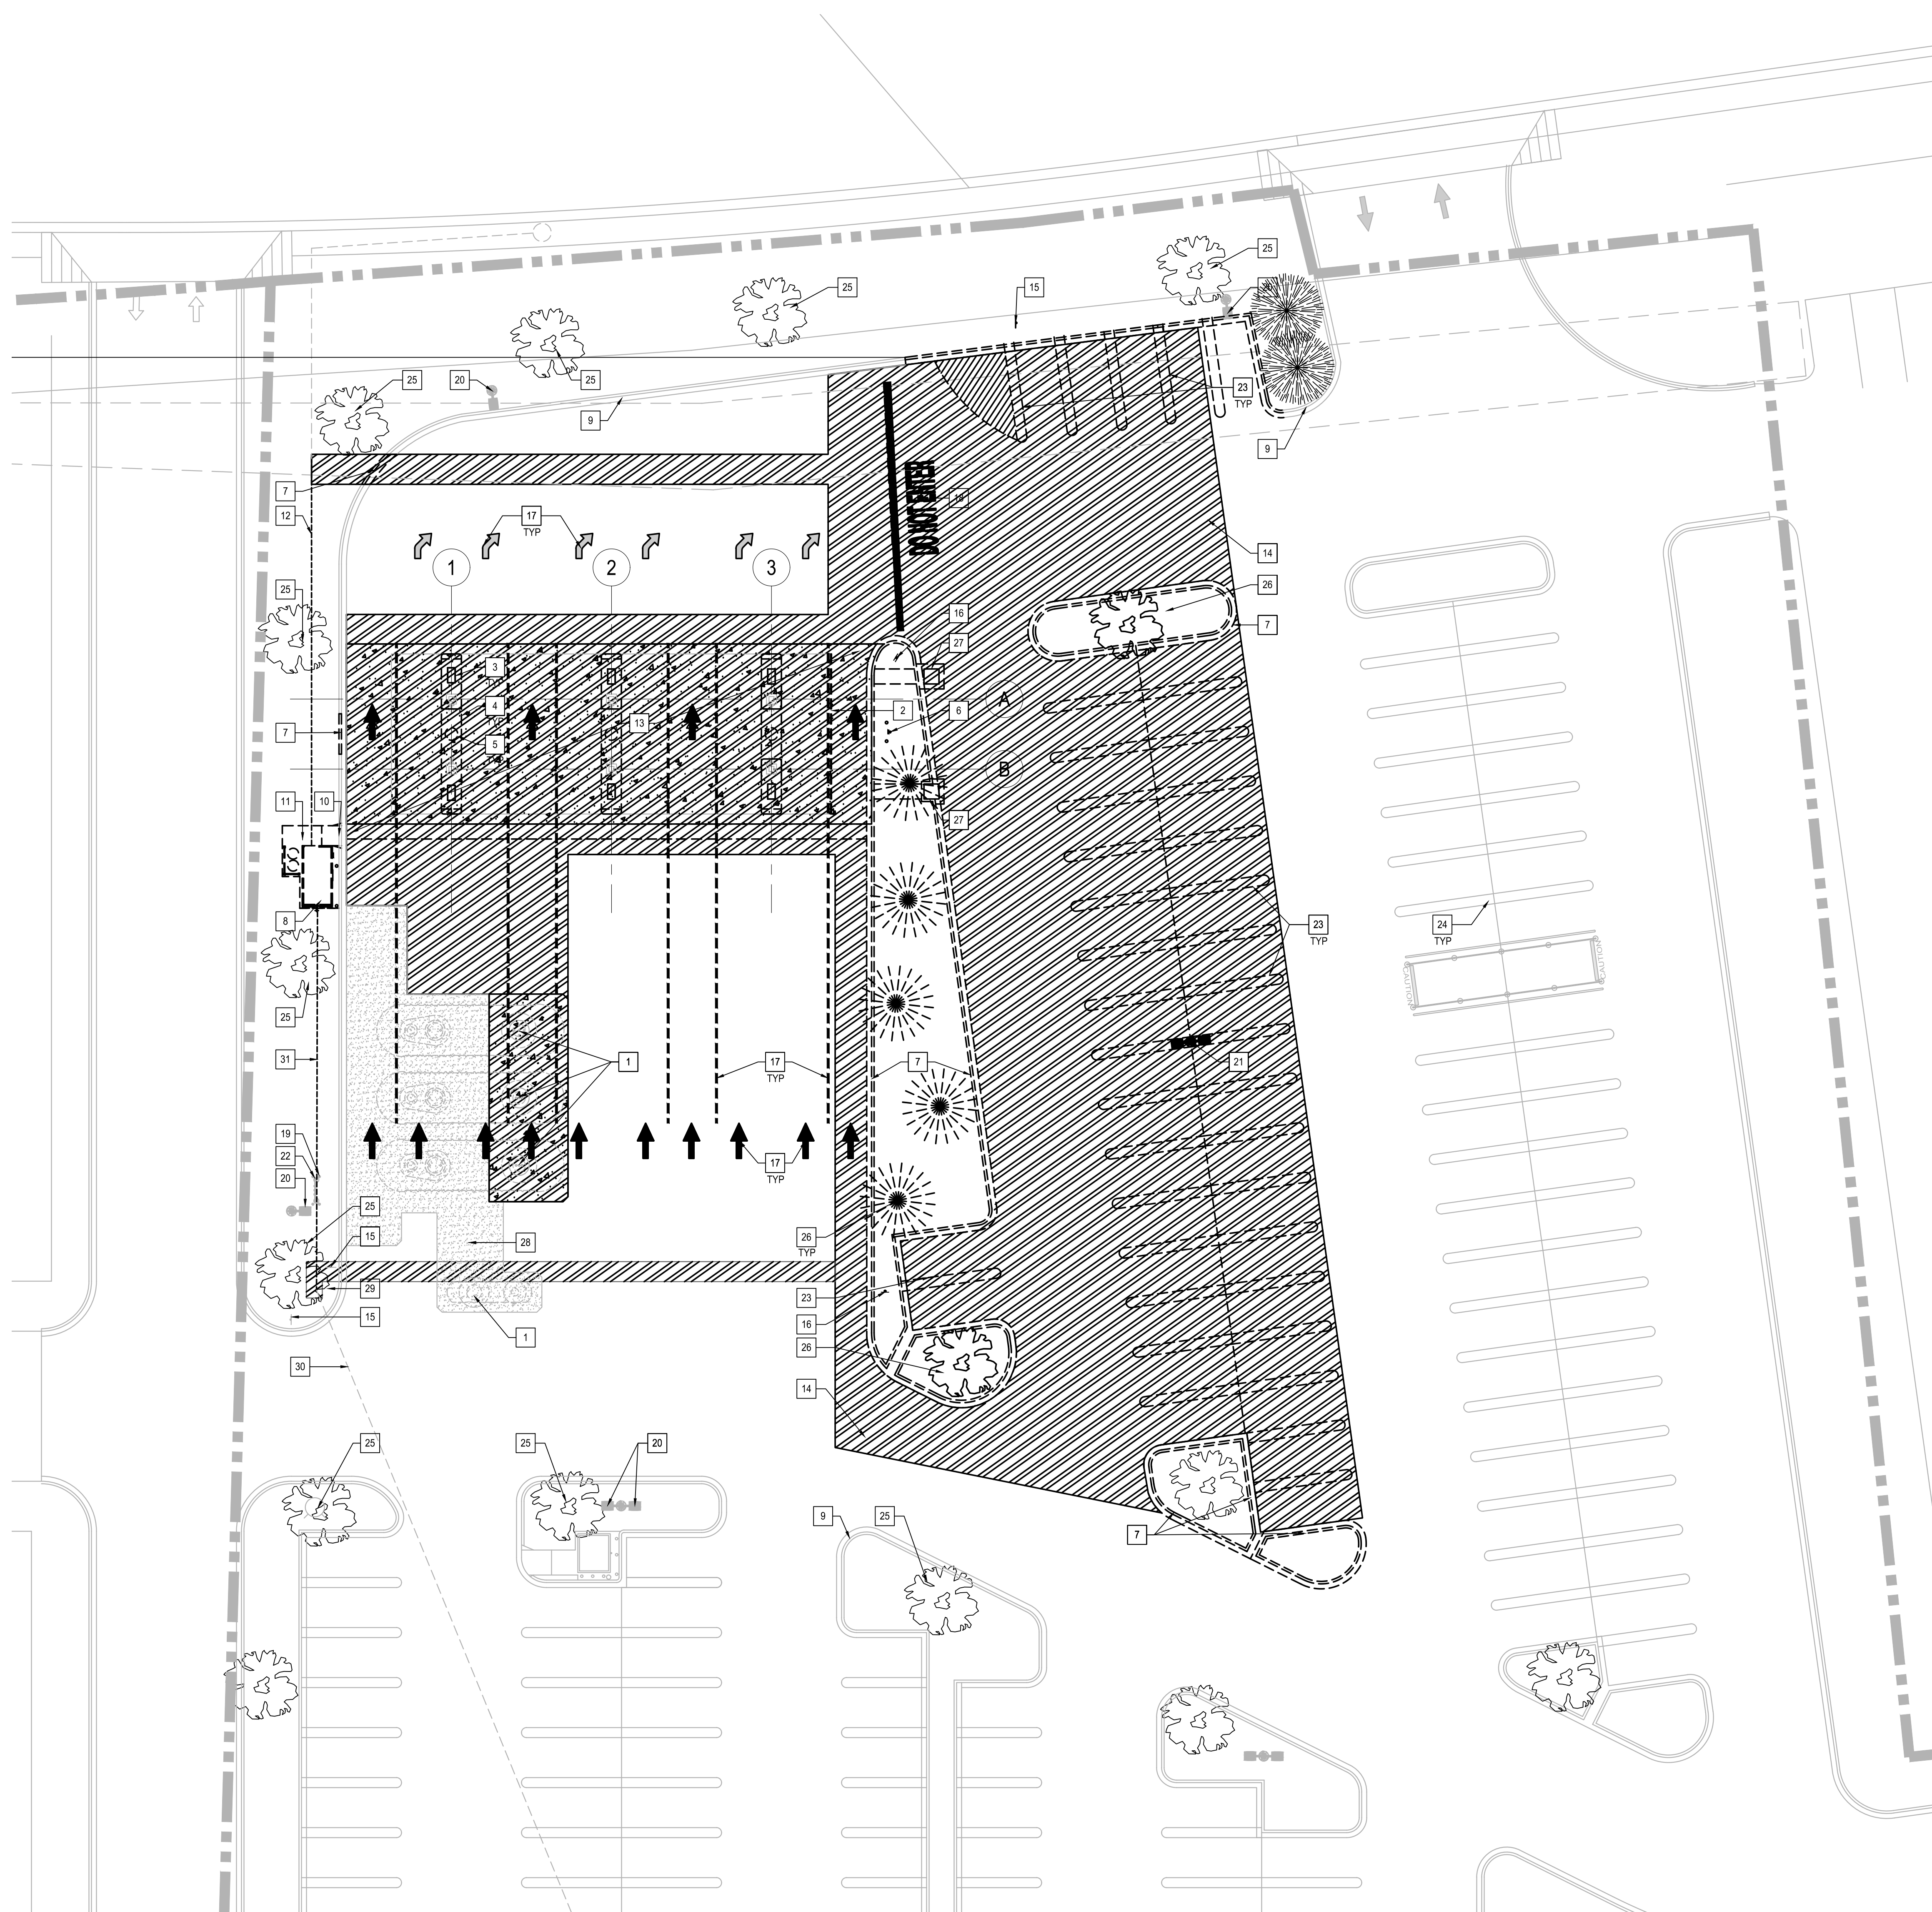


1	EXISTING UNDERGROUND STORAGE TANKS TO REMAIN
2	DEMO AND PREP EXISTING FUEL CANOPY ON THE EAST SIDE FOR EXPANSION.
3	EXISTING MULTI-PRODUCT DISPENSER TO BE REPLACED.
4	EXISTING CONCRETE DISPENSER ISLAND TO BE DEMOLISHED.
5	EXISTING WASTE RECEPTOR TO BE REMOVED AND RETAINED FOR RE-INSTALLATION.
6	EXISTING EMERGENCY SHUT OFF SWITCH TO BE REMOVED
7	EXISTING CURB AND GUTTER TO BE REMOVED.
8	EXISTING CONTROLLER ENCLOSURE AND ASSOCIATED EQUIPMENT TO BE DEMOLISHED / REMOVED
9	EXISTING CURB TO REMAIN
10	EXISTING CURB TO BE REMOVED
11	EXISTING CONCRETE WALKWAY TO BE REMOVED
12	EXISTING CONDUIT WIRES TO BE TERMINATED AND CAPPED.
13	REMOVE AND REPLACE EXISTING CONCRETE SLAB.
14	LIMITS OF DISTURBANCE: REMOVE AND REPLACE EXISTING ASPHALT AS NEEDED FOR NEW PIPING
15	EXISTING STOP SIGN TO BE REMOVED.
16	EXISTING STOP SIGN TO BE RELOCATED.
17	REMOVE EXISTING PAINT STRIPING.
18	EXISTING PAINTED "DO NOT ENTER" SIGN TO BE REMOVED
19	EXISTING BOLLARD TO REMAIN
20	EXISTING LIGHT POLE & LIGHTS TO REMAIN
21	EXISTING LIGHT POLE & LIGHTS TO BE REMOVED
22	EXISTING VENT RISER TO REMAIN
23	EXISTING PARKING STALLS TO BE REMOVED
24	EXISTING PARKING STALLS TO REMAIN
25	EXISTING TREE TO REMAIN
26	EXISTING TREE TO BE REMOVED
27	EXISTING METAL COVER TO BE REMOVED
28	EXISTING CONDUIT TO REMAIN
29	NEW COMMUNICATION CONDUIT PULL BOX - GC TO VERIFY IN FIELD OR INSTALL NEW ONE
30	EXISTING COMMUNICATION CONDUIT TO WAREHOUSE TO REMAIN - GC TO VERIFY IN FIELD
31	EXISTING COMMUNICATION CONDUIT TO BE REMOVED

 EXTENT OF CONCRETE TO BE REMOVED AS NEEDED FOR NEW PRODUCT PIPING
 FULL DEPTH PAVEMENT TO BE REMOVED
 EXISTING CONCRETE TO REMAIN

- THE BUILDING WILL BE OCCUPIED AND IN FULL USE BY THE OWNER DURING CONSTRUCTION
1. CONSTRUCTION THAT MAY AFFECT THE PUBLIC SHALL BE DONE DURING OFF-HOURS
2. AREAS OF DEMOLITION SHALL INCLUDE, BUT ARE NOT LIMITED TO ANY STRUCTURAL, MECHANICAL, ELECTRICAL, PIPING, AND/OR FURNITURE. THE CONTRACTOR SHALL COMPLETE THE DEMOLITION WORK. THE CONTRACTOR IS TO REMOVE ALL WALLS, BOLLARDS, ASSOCIATED WITH DEMOLITION OF AREAS SHOWN.
3. ALL EXISTING ITEMS NOT ALLOWED FOR REUSE SHALL BE OFFERED IN GOOD CONDITION TO THE OWNER. DURING THE BIDDING PERIOD, COORDINATE AND VERIFY WITH THE OWNER AS TO WHICH ITEMS ARE TO BE SALVAGED.
4. DO NOT INTERRUPT ANY ELECTRICAL, PIPING, FIRE SPRINKLER, ETC. WITHOUT PRIOR WRITTEN APPROVAL OF THE OWNER.
5. PROVIDE AND MAINTAIN EGRESS PATHS THROUGHOUT CONSTRUCTION INCLUDING, BUT NOT LIMITED TO EXIT SIGNS, EMERGENCY EXIT LIGHTS, AND EGRESS MARKING. THE WORK AREA PRIOR TO CLOSING ANY EGRESS OPENINGS AND/OR EGRESS PATHS DURING DEMOLITION/CONSTRUCTION.
6. THE CONTRACTOR SHALL LOCATE ALL EXISTING UNDERGROUND UTILITIES WITHIN PROXIMITY TO THE WORK AREA PRIOR TO EXCAVATION.
7. EXISTING UTILITIES SHOWN HAVE BEEN OBTAINED FROM AVAILABLE RECORDS AND ARE SHOWN FOR CONVENIENCE ONLY. VERIFY ALL INVERT ELEVATIONS AT POINTS OF CONNECTIONS OF NEW UTILITIES TO EXISTING UTILITIES. STATE WORK AREA.
8. PROVIDE TEMPORARY DUST PARTITIONS AS NECESSARY TO PREVENT DUST AND DEBRIS FROM SETTLING ON ADJACENT AREAS NOT UNDER CONSTRUCTION. REVIEW WITH AND OBTAIN OWNER APPROVAL FOR FLOOR LOCATIONS.
9. ALL UTILITIES AND PIPING BELOW THE FLOOR AS REQUIRED. CONTRACTOR IS RESPONSIBLE FOR FLOOR PATCHING.
10. THE CONTRACTOR IS RESPONSIBLE FOR REPAIRING OR REPLACING ITEMS DAMAGED DURING DEMOLITION AND CONSTRUCTION.
11. WHEN CUTTING AND PATCHING, THE CONTRACTOR SHALL USE METHODS LEAST LIKELY TO DAMAGE ELEMENTS RETAINED OR ADJACENT SURFACES. CUT HOLES AND SLOTS AS SMALL AS POSSIBLE, NEATLY, TO SIZE REQUIRED AND WITH MINIMUM DISTURBANCES OF ADJACENT MATERIALS.
12. WHERE EXISTING CONSTRUCTION IS REMOVED, CUT OR OTHERWISE INTERRUPTED, PATCH TO MATCH THE EXISTING ADJACENT SURFACES. SEAMS TO BE AS INVISIBLE AS PRACTICAL. REFINISHES SHALL BE MATCHED TO THE NEAREST VISUAL BREAK LINES SUCH AS CORNERS, CEILING LINES, TOP OF BASE, ETC.
13. WHERE NEW WORK ABUTS OR ALIGNS WITH EXISTING, PERFORM A SMOOTH AND EVEN TRANSITION. PATCHED WORK TO MATCH EXISTING ADJACENT WORK IN TEXTURE AND APPEARANCE.
14. REMOVE AND REPLACE AREAS, SURFACES OR ITEMS THAT CANNOT BE SATISFACTORILY REPAIRED.
15. AS A MINIMUM, THE LEVEL OF WORKSHIP SHOULD MATCH THE GENERAL LEVEL OF EXISTING WORKSHIP.
16. UNLESS SHOWN ON THE DRAWINGS OTHERWISE, DO NOT SUPPORT OR SUSPEND ITEMS, EQUIPMENT, HANGERS, ETC. FROM EXISTING STRUCTURAL MEMBERS (BEAMS, TRUSSES, JOIST, ETC.) WITHOUT WRITTEN APPROVAL OF A LICENSED STRUCTURAL ENGINEER.
17. DO NOT CUT OR DRILL ANY STRUCTURAL MEMBER (PARTICULARLY ROOF JOIST) WITHOUT WRITTEN APPROVAL OF A LICENSED STRUCTURAL ENGINEER.
18. SHORING OF STRUCTURAL FOUNDATIONS, STRUCTURES, AND/OR TRENCING REQUIRED TO COMPLETE THE WORK DESCRIBED IN THE DOCUMENTS IS CONSIDERED A MEANS, METHOD OR TECHNIQUE AND IS THE SOLE RESPONSIBILITY OF THE CONTRACTOR.
19. THE CONTRACTOR MAY REQUIRE A LICENSED ENGINEER TO SUPERVISE, APPROVE, AND/OR PROVIDE DRAWINGS FOR STRUCTURAL FOUNDATIONS, STRUCTURES, AND/OR TRENCING. IT IS THE RESPONSIBILITY OF THE CONTRACTOR TO COORDINATE WITH THE ENGINEER DIRECTLY AND THE CONTRACT SHALL BE IN FULL FORCE AND EFFECT.
20. ALL SYSTEMS AND SERVICES ARE TO BE LEFT OPERATIONAL PRIOR TO THE END OF EACH WORKDAY.
21. THE CONTRACTOR SHALL REMOVE ALL RUBBLE AND DEBRIS FROM THE JOBSITE DAILY AND LEAVE THE BUILDING AND GROUNDS BROOM CLEAN UPON COMPLETION OF THE WORK.

OPERATIONAL PHASING NOTES


1. THE CONTRACTOR TO SUBMIT PHASING PLAN AT BID. THE CONTRACTOR SHALL CONFIRM THE OPERATIONAL PHASING WITH THE OWNER PRIOR TO STARTING CONSTRUCTION.
2. THE PHASING SHOWN IS NOT INTENDED TO REPRESENT OR DICTATE CONSTRUCTION SEQUENCE OR MEANS. MEANS SHALL BE DETERMINED BY THE CONTRACTOR.
3. THE CONTRACTOR IS RESPONSIBLE FOR COORDINATING ALL CONSTRUCTION PHASING SO AS NOT TO IMPACT THE OPERATIONS.
4. REMOVE WALLS, BOLASTERS, BRACINGS, ELECTRICAL, ETC. AND CAP UTILITIES BELOW THE FLOOR AS REQUIRED TO ACHIEVE THE OPERATIONAL.
5. PROVIDE TEMPORARY UTILITIES AS REQUIRED DURING PHASING.
6. REMOVE WALLS, BOLASTERS, BRACINGS, ELECTRICAL, ETC. AND COVERING OF THE EXISTING EXTERIOR SIGNAGE. THE CONTRACTOR SHALL PROVIDE A TEMPORARY "COSTCO WHOLESALE" SIGNAGE (OR SIZE COMPARABLE TO EXISTING SIGN) UNTIL PERMANENT SIGN IS INSTALLED.
7. THE CONTRACTOR SHALL PROVIDE TEMPORARY LIGHTING TO PROVIDE ILLUMINATION FOR THE PHASING. CONFIRM LOCATIONS WITH THE OWNER.

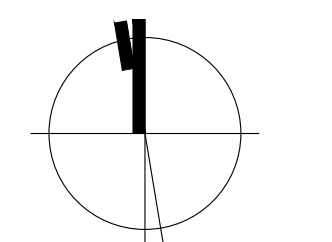


0 8' 16' 32'

$\frac{1}{16}'' = 1'-0''$


DOUGLAS E. BROOKBANK, ARCHITECT

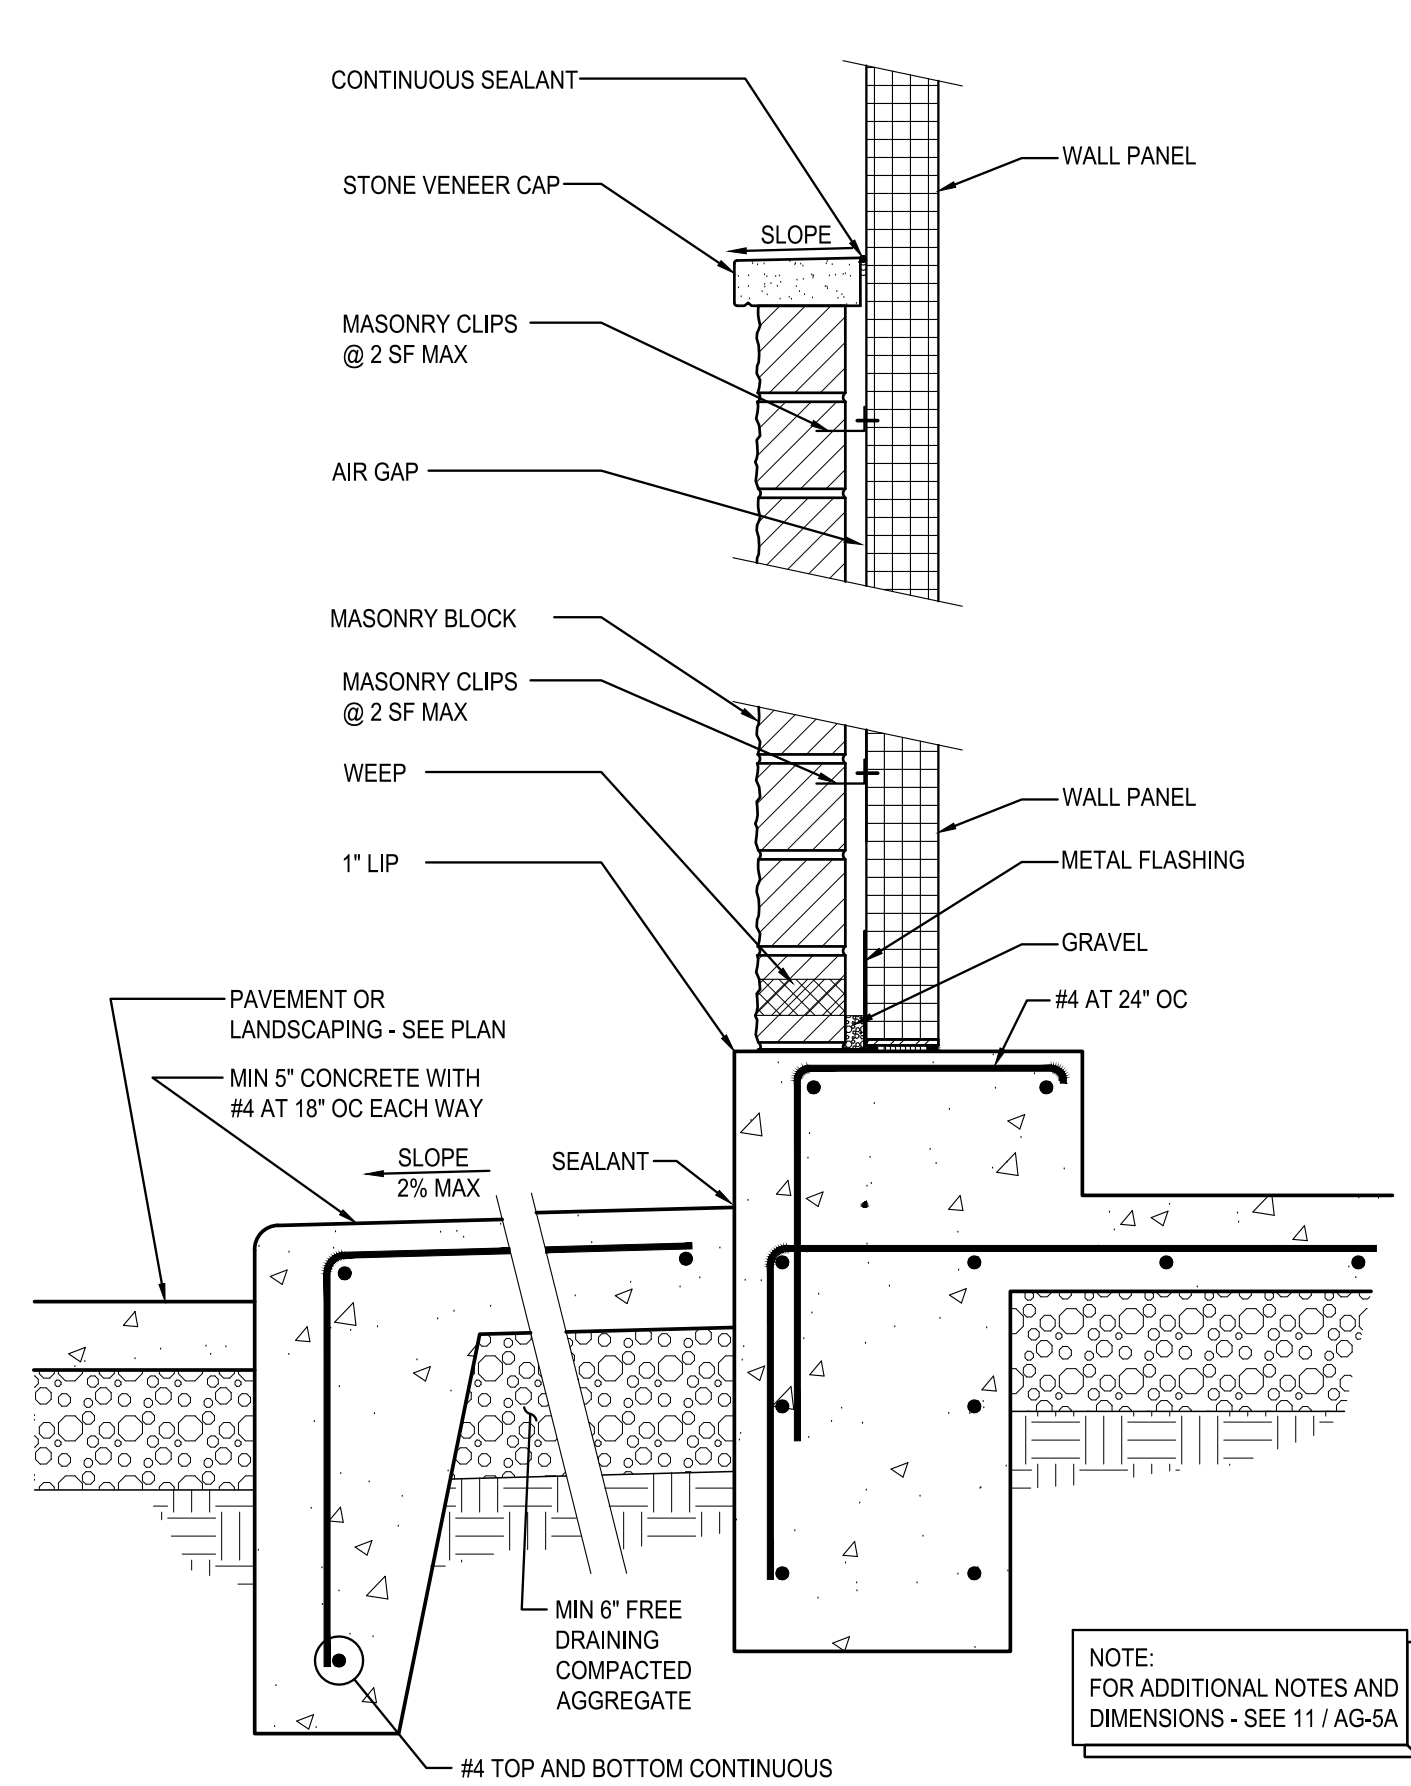


6 TYPICAL EDGE OF WALK
SCALE: 1-1/2" = 1'-0" 1021

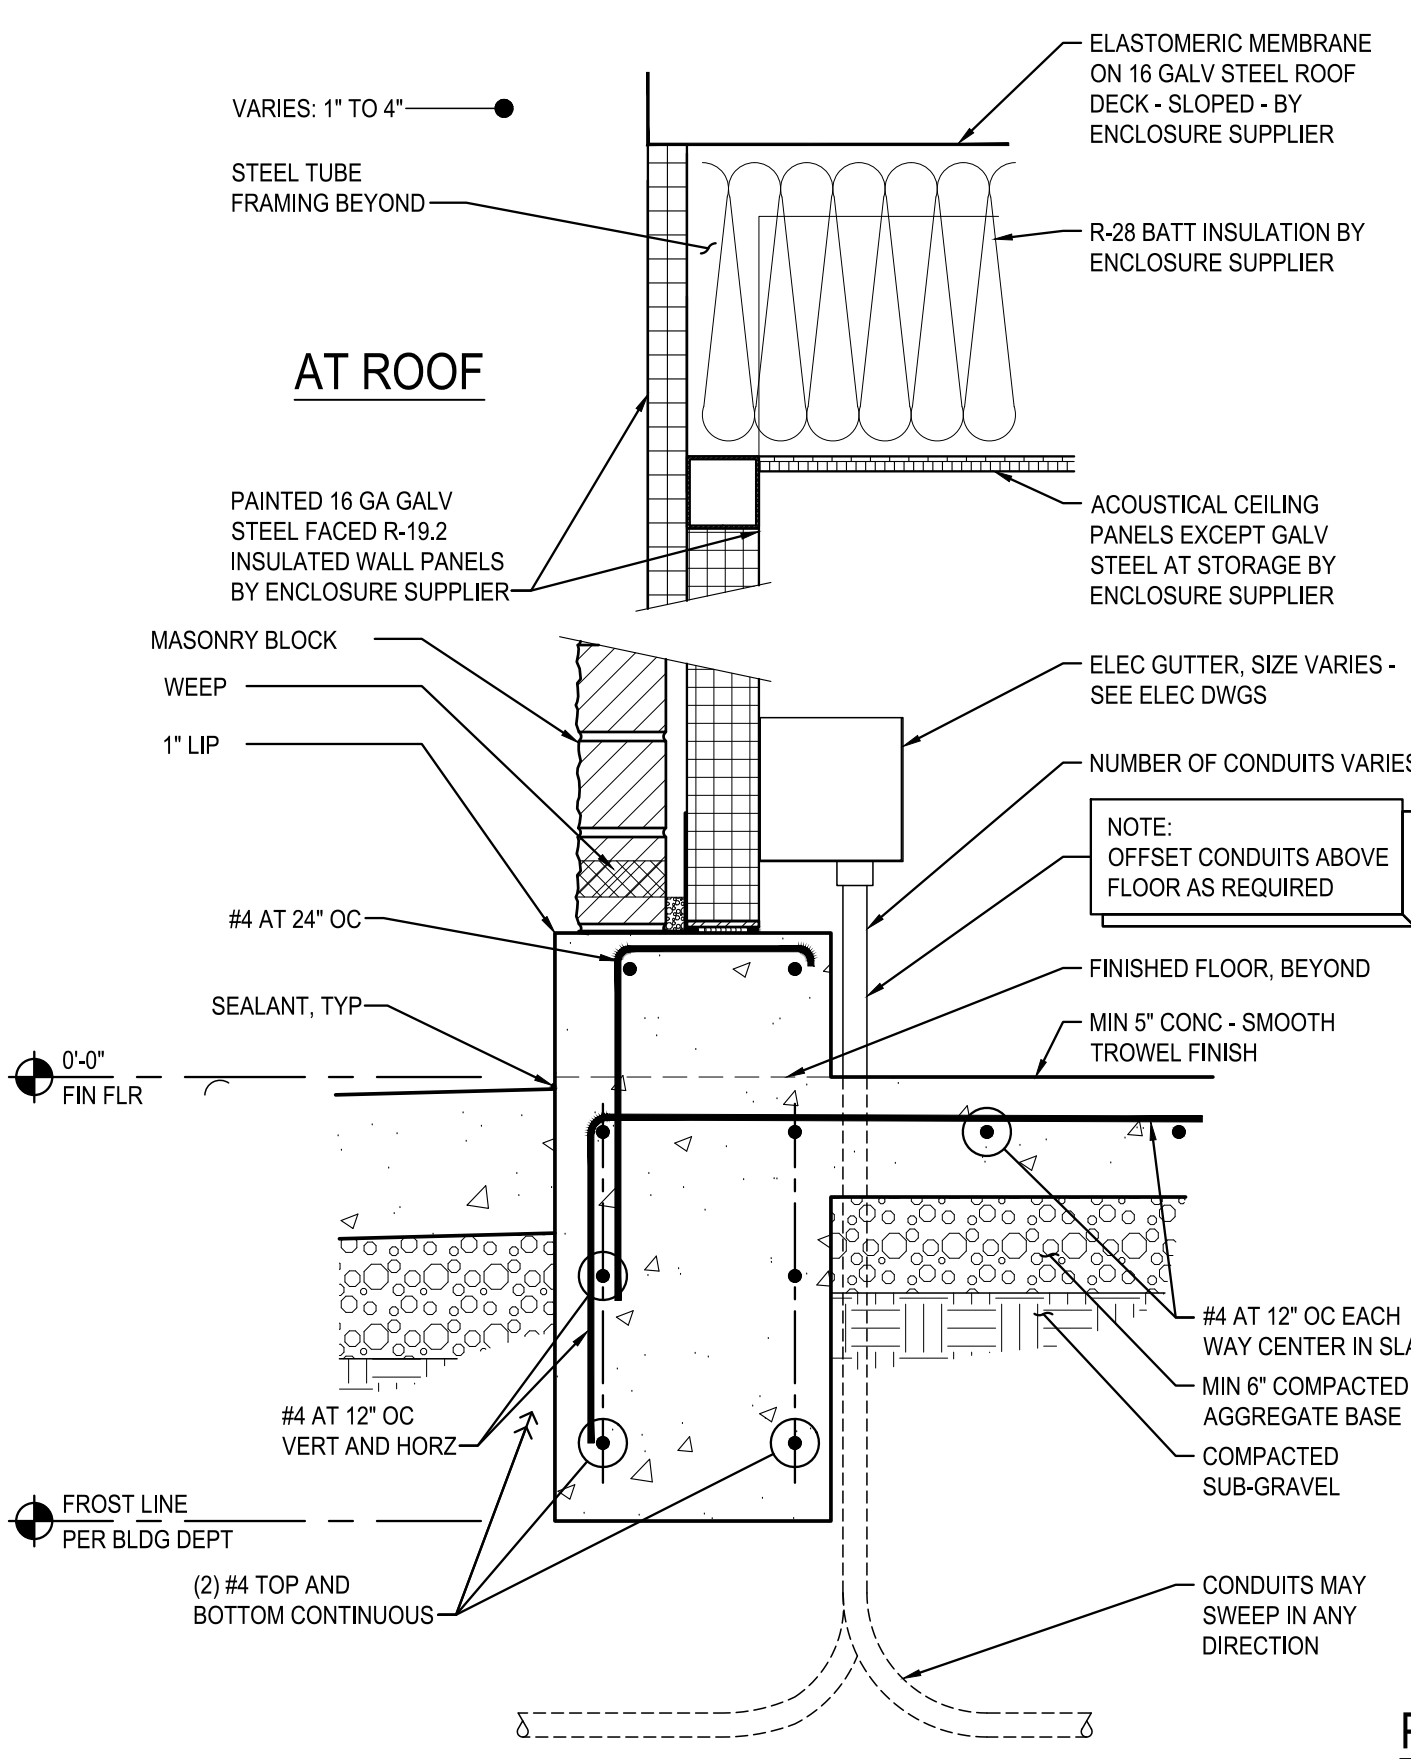


11 TYPICAL WALL
SCALE: 1-1/2" = 1'-0" 0421

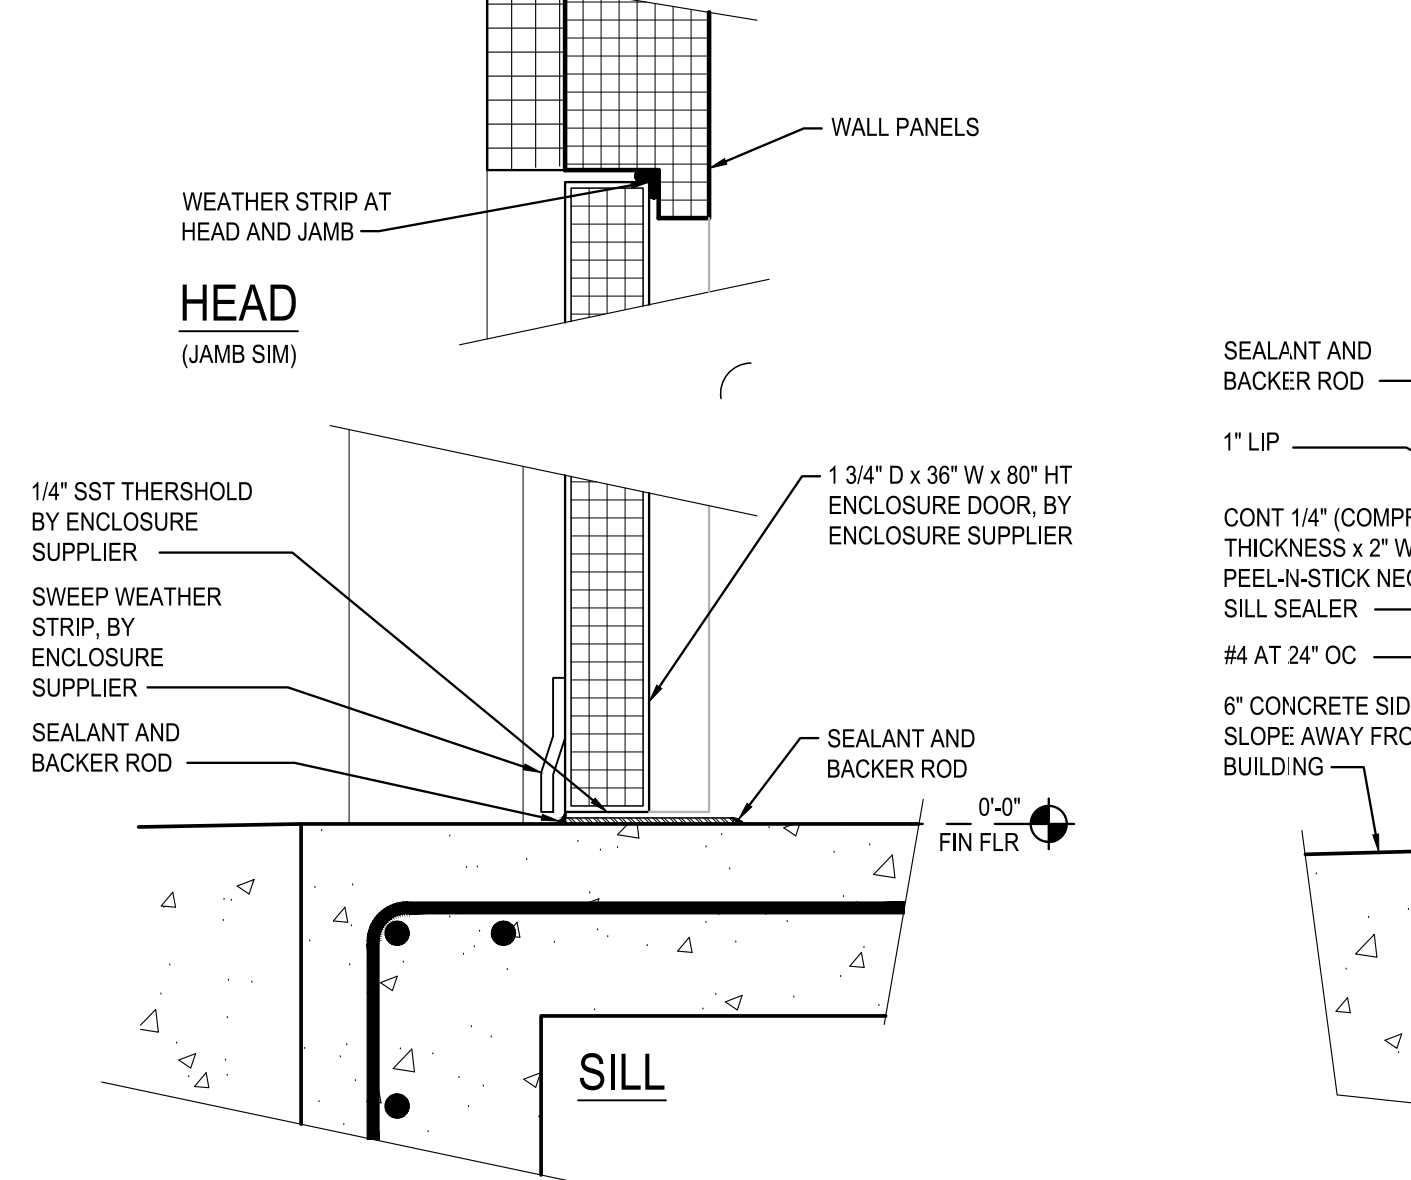


16 FOUNDATION AT DOOR
SCALE: 3" = 1'-0" 0721

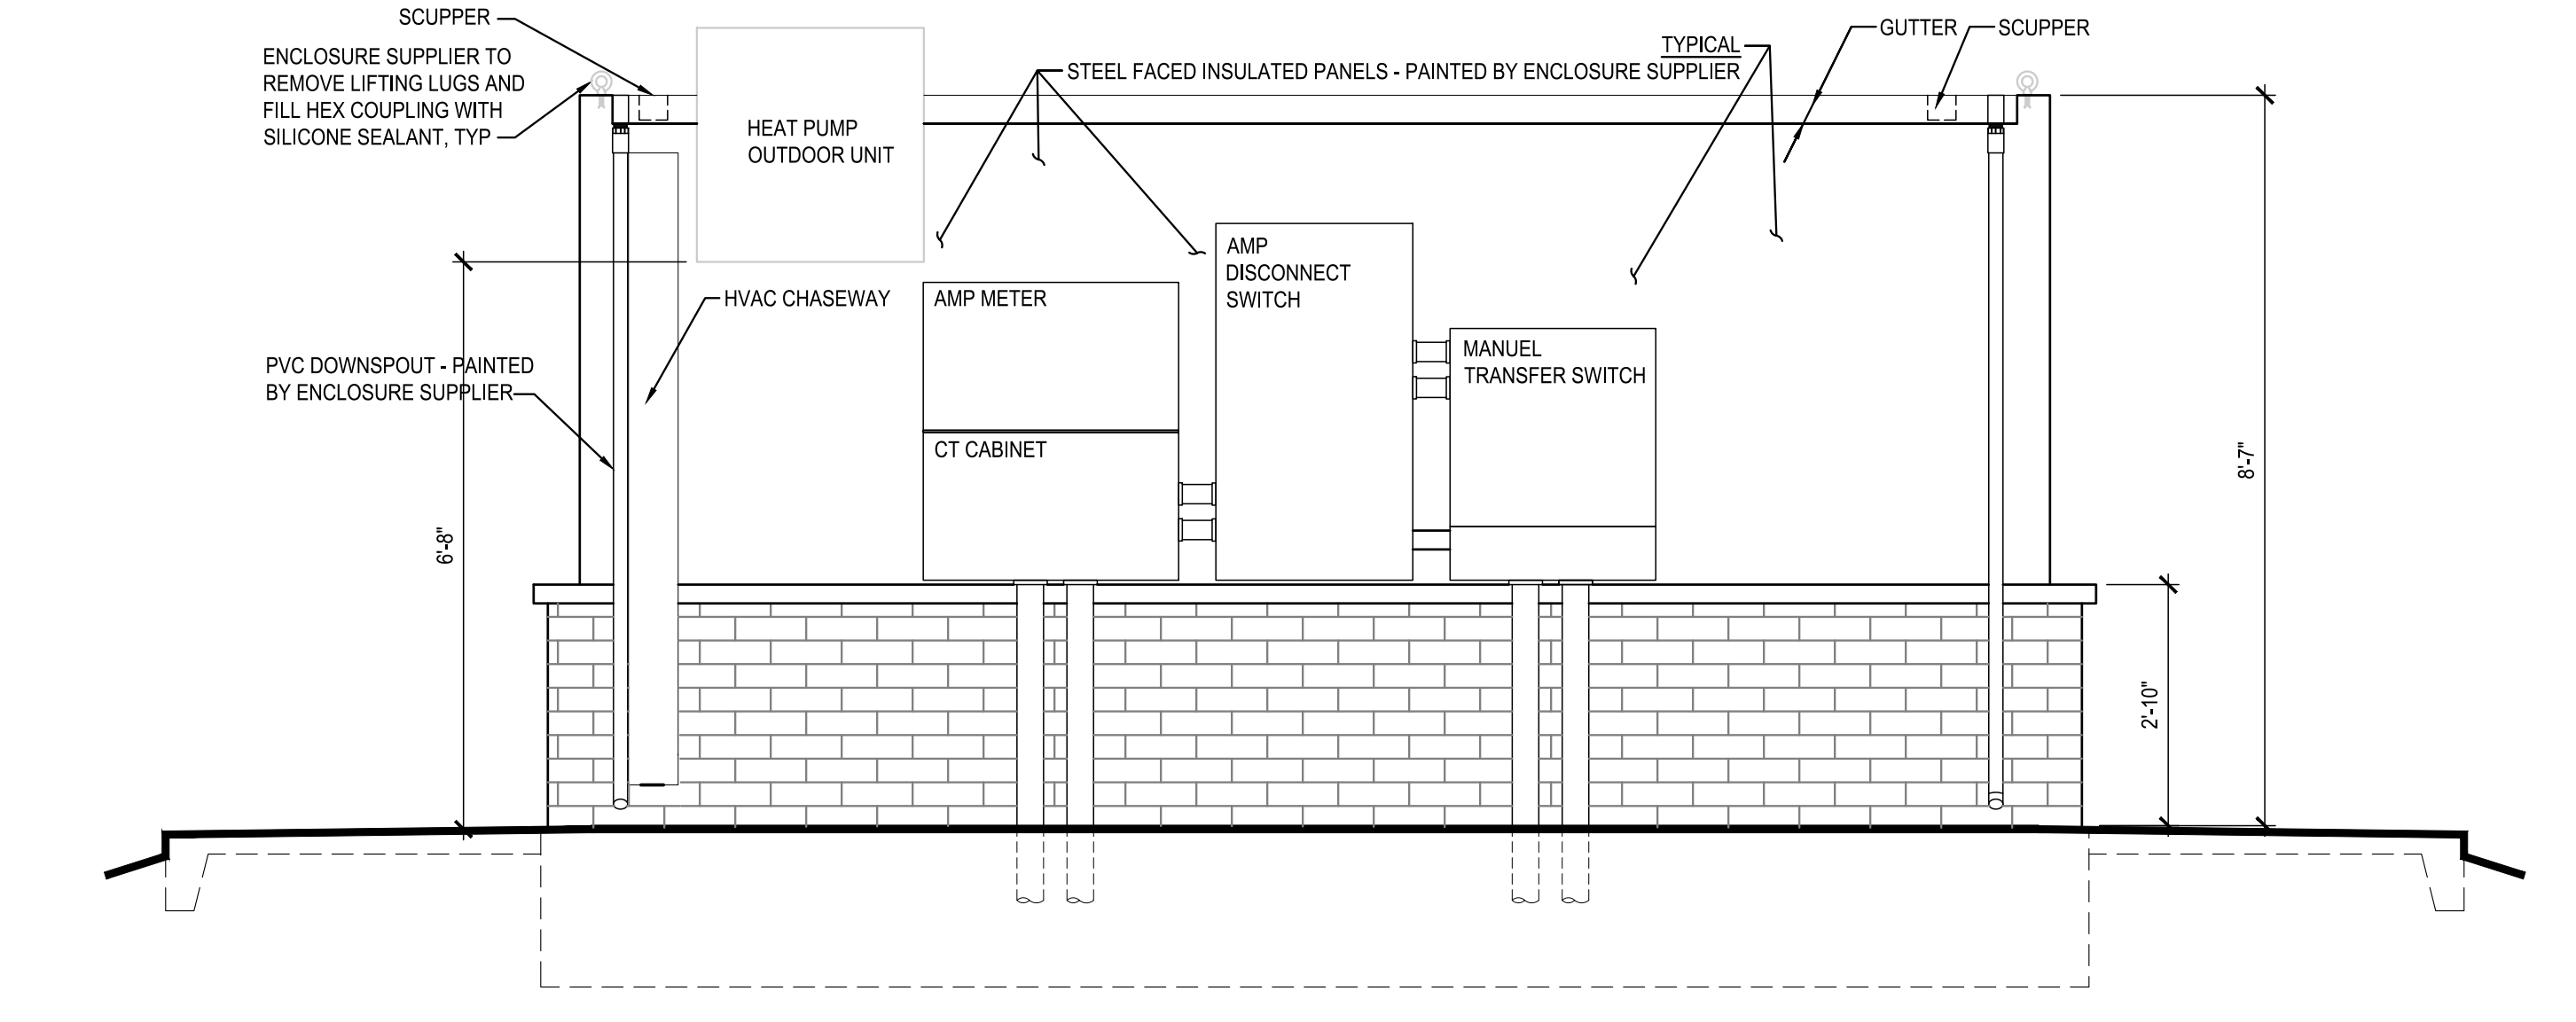


2 SIDE FACING AWAY FROM CANOPY
SCALE: 1/2" = 1'-0" 1121

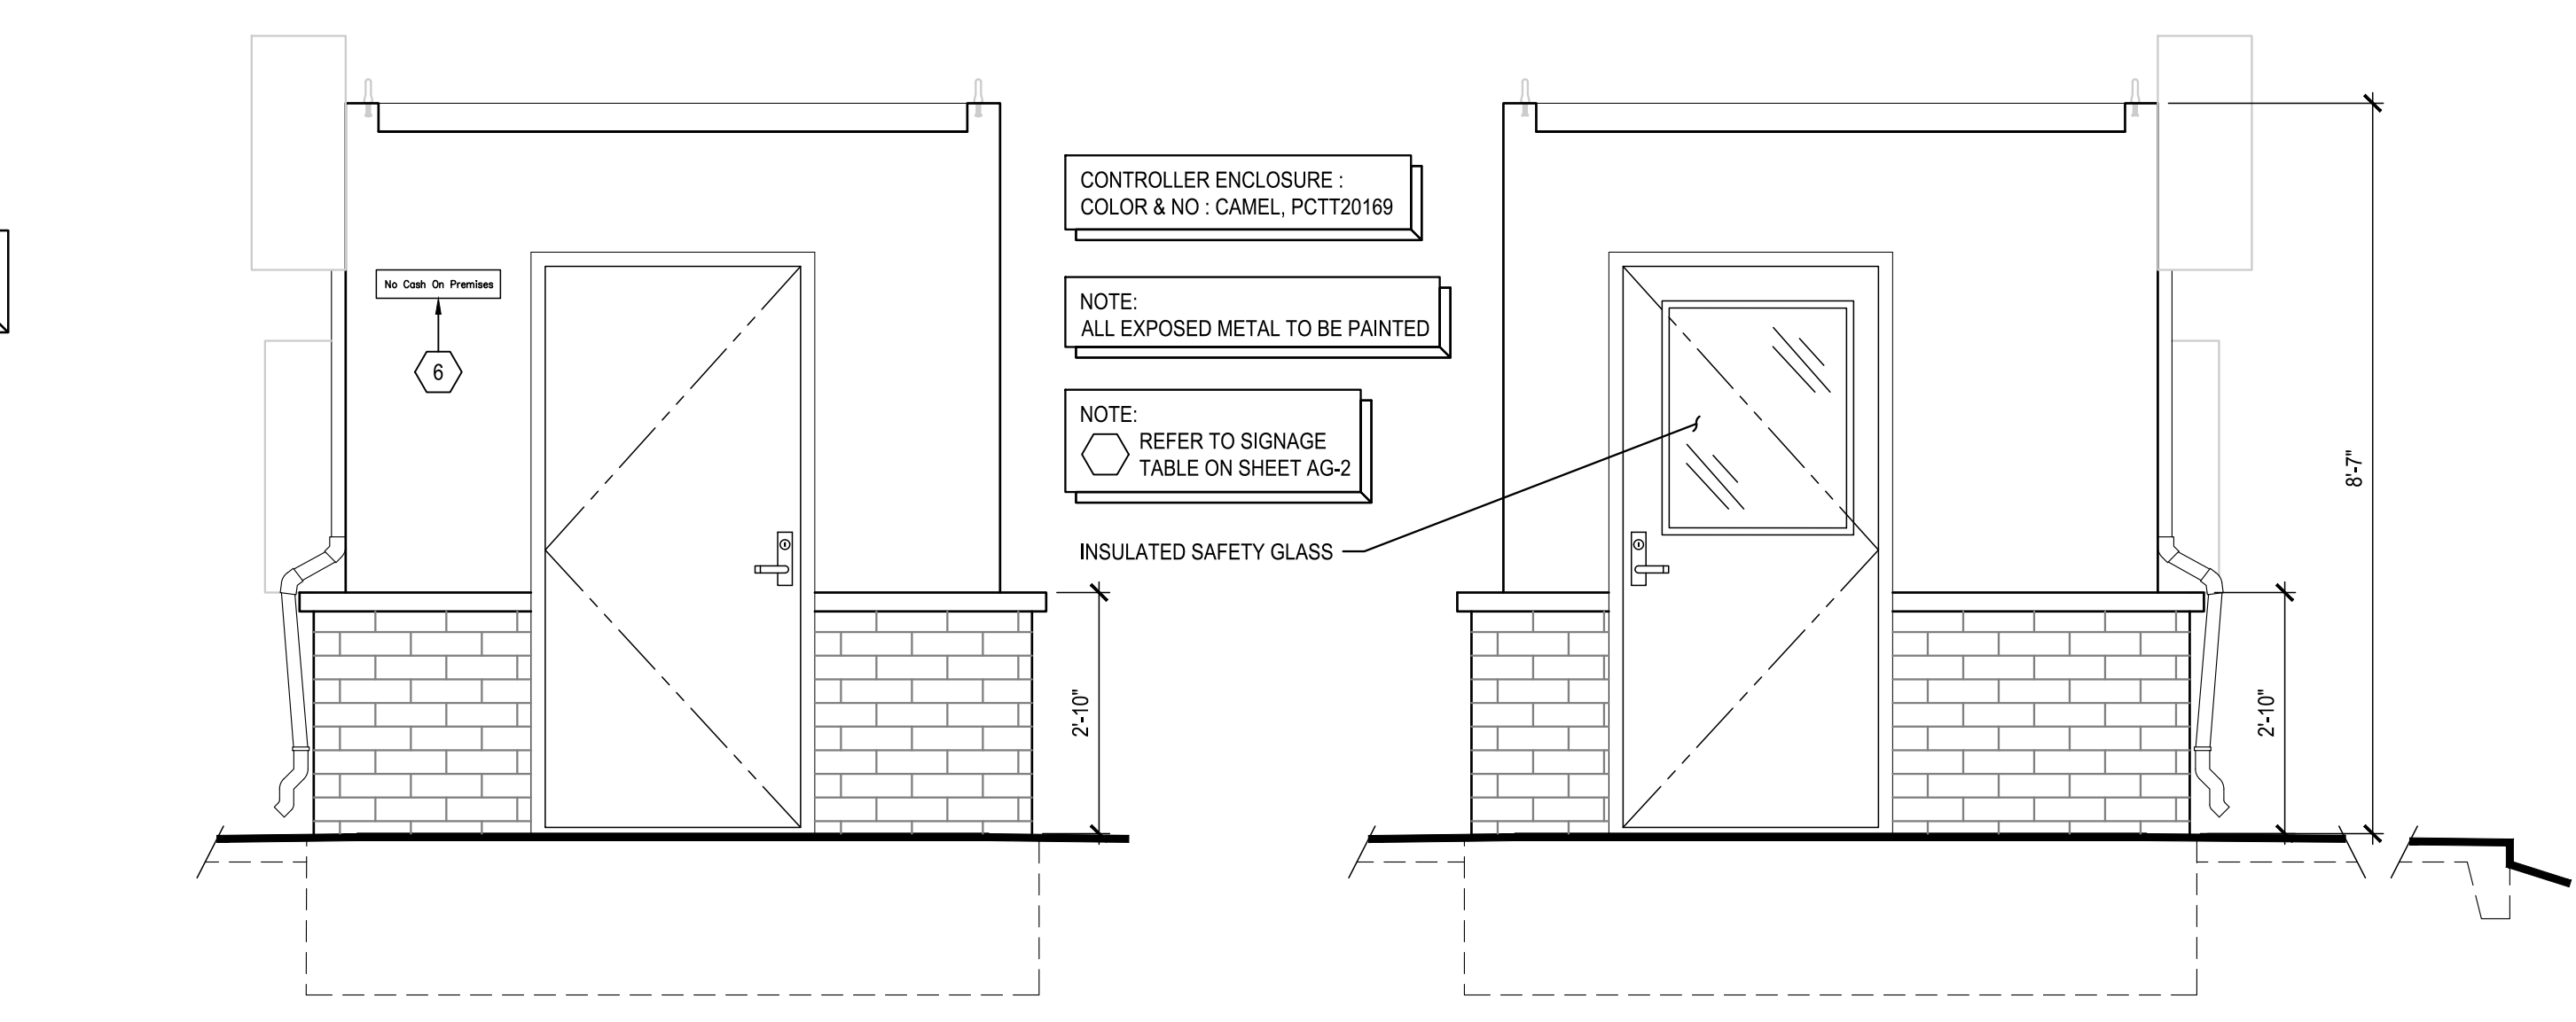


7 STORAGE ENTRY
SCALE: 1/2" = 1'-0" 1222

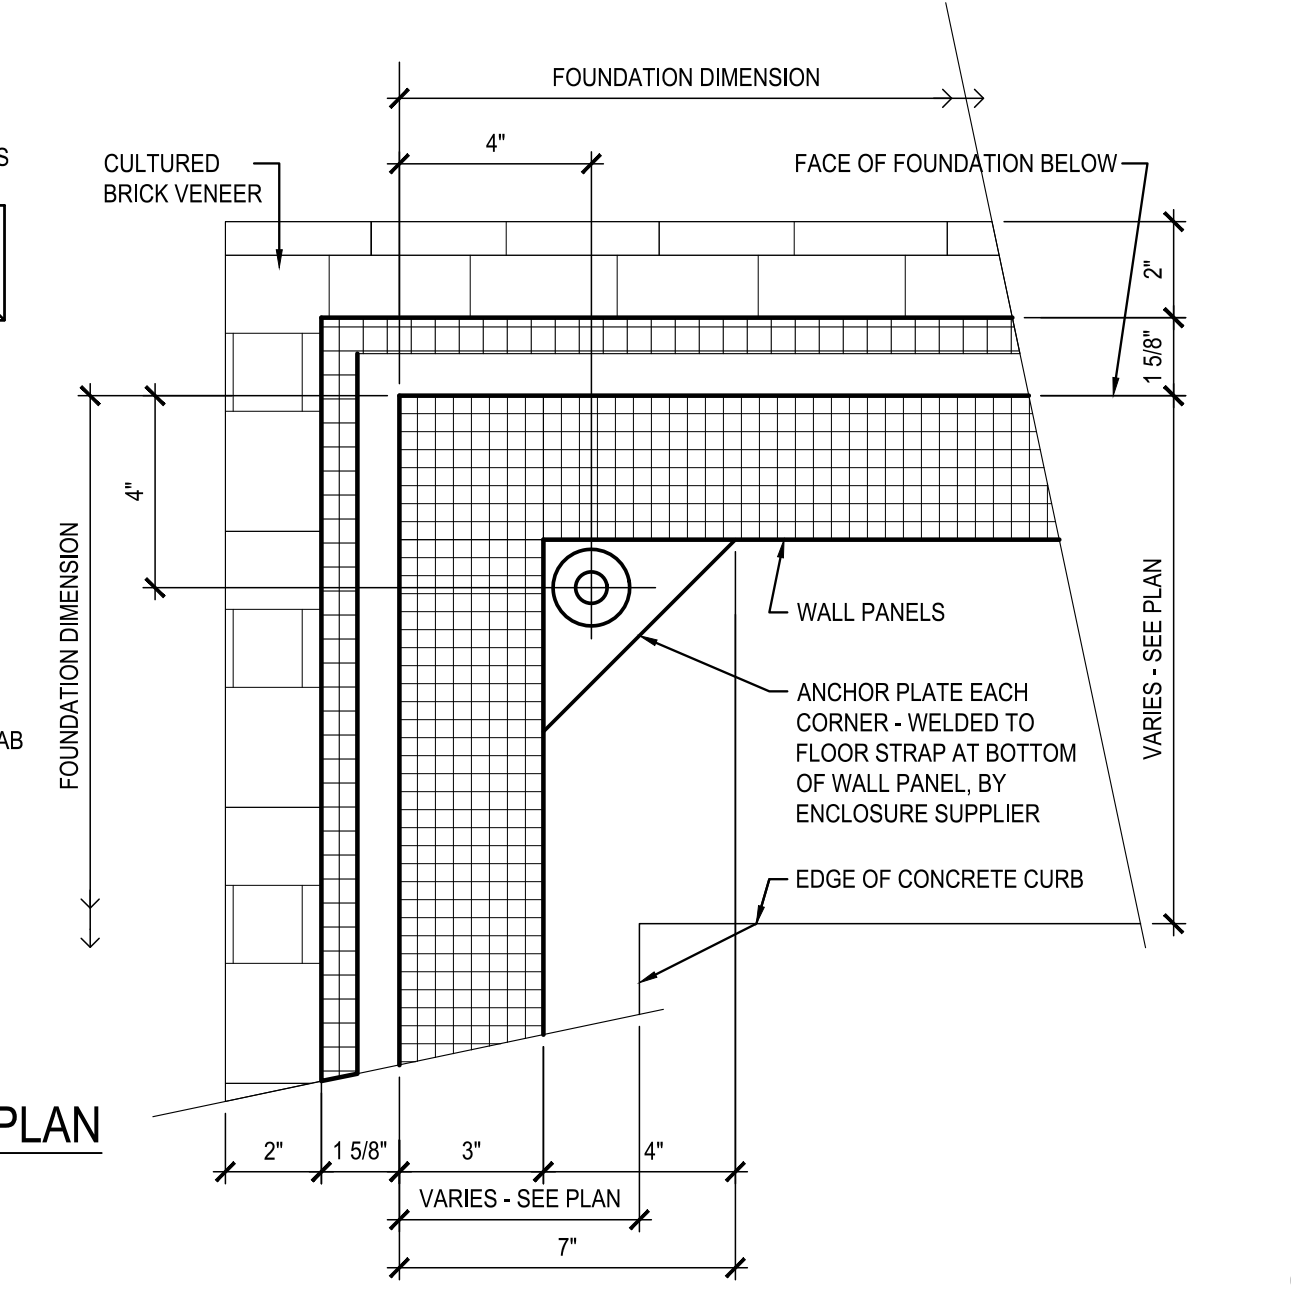


17 FOUNDATION CORNER
SCALE: 3" = 1'-0" 0421

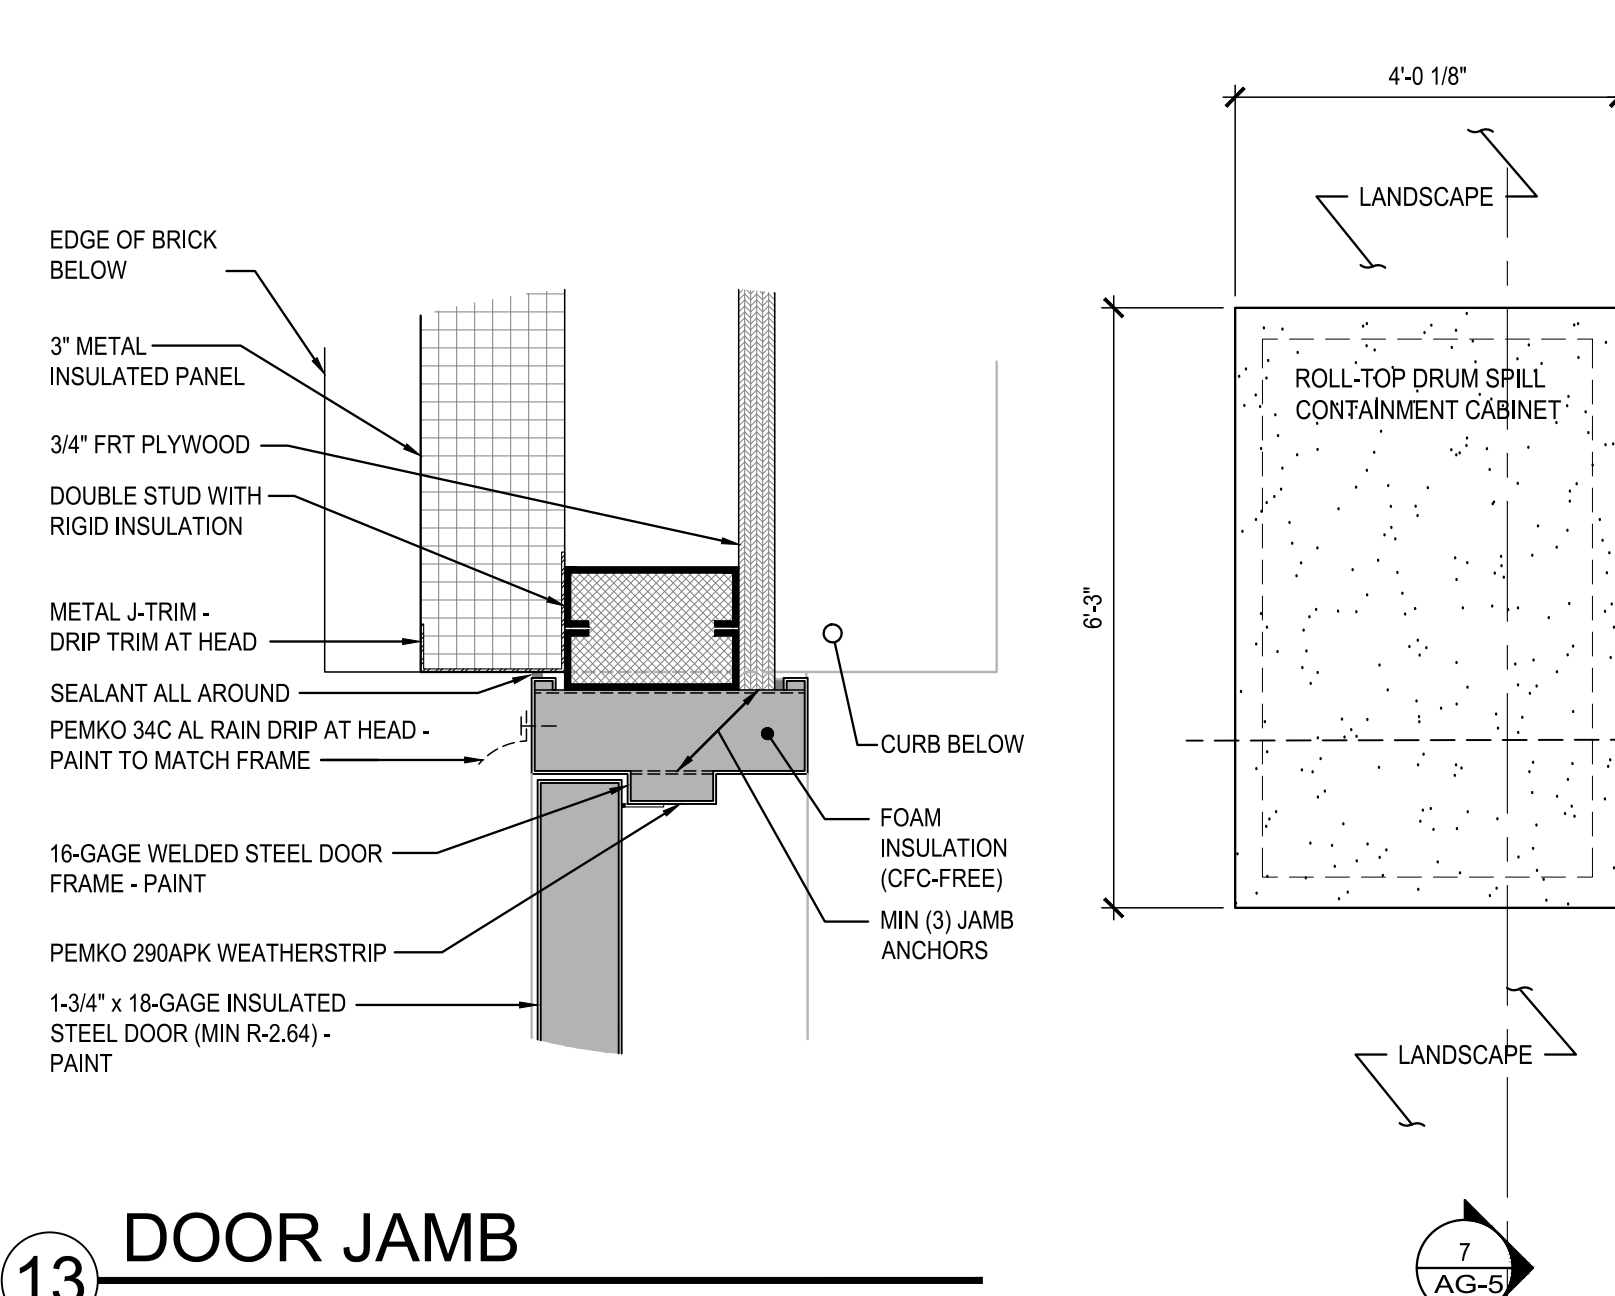


13 DOOR JAMB
SCALE: 3" = 1'-0" (HEAD SIMILAR) 0122

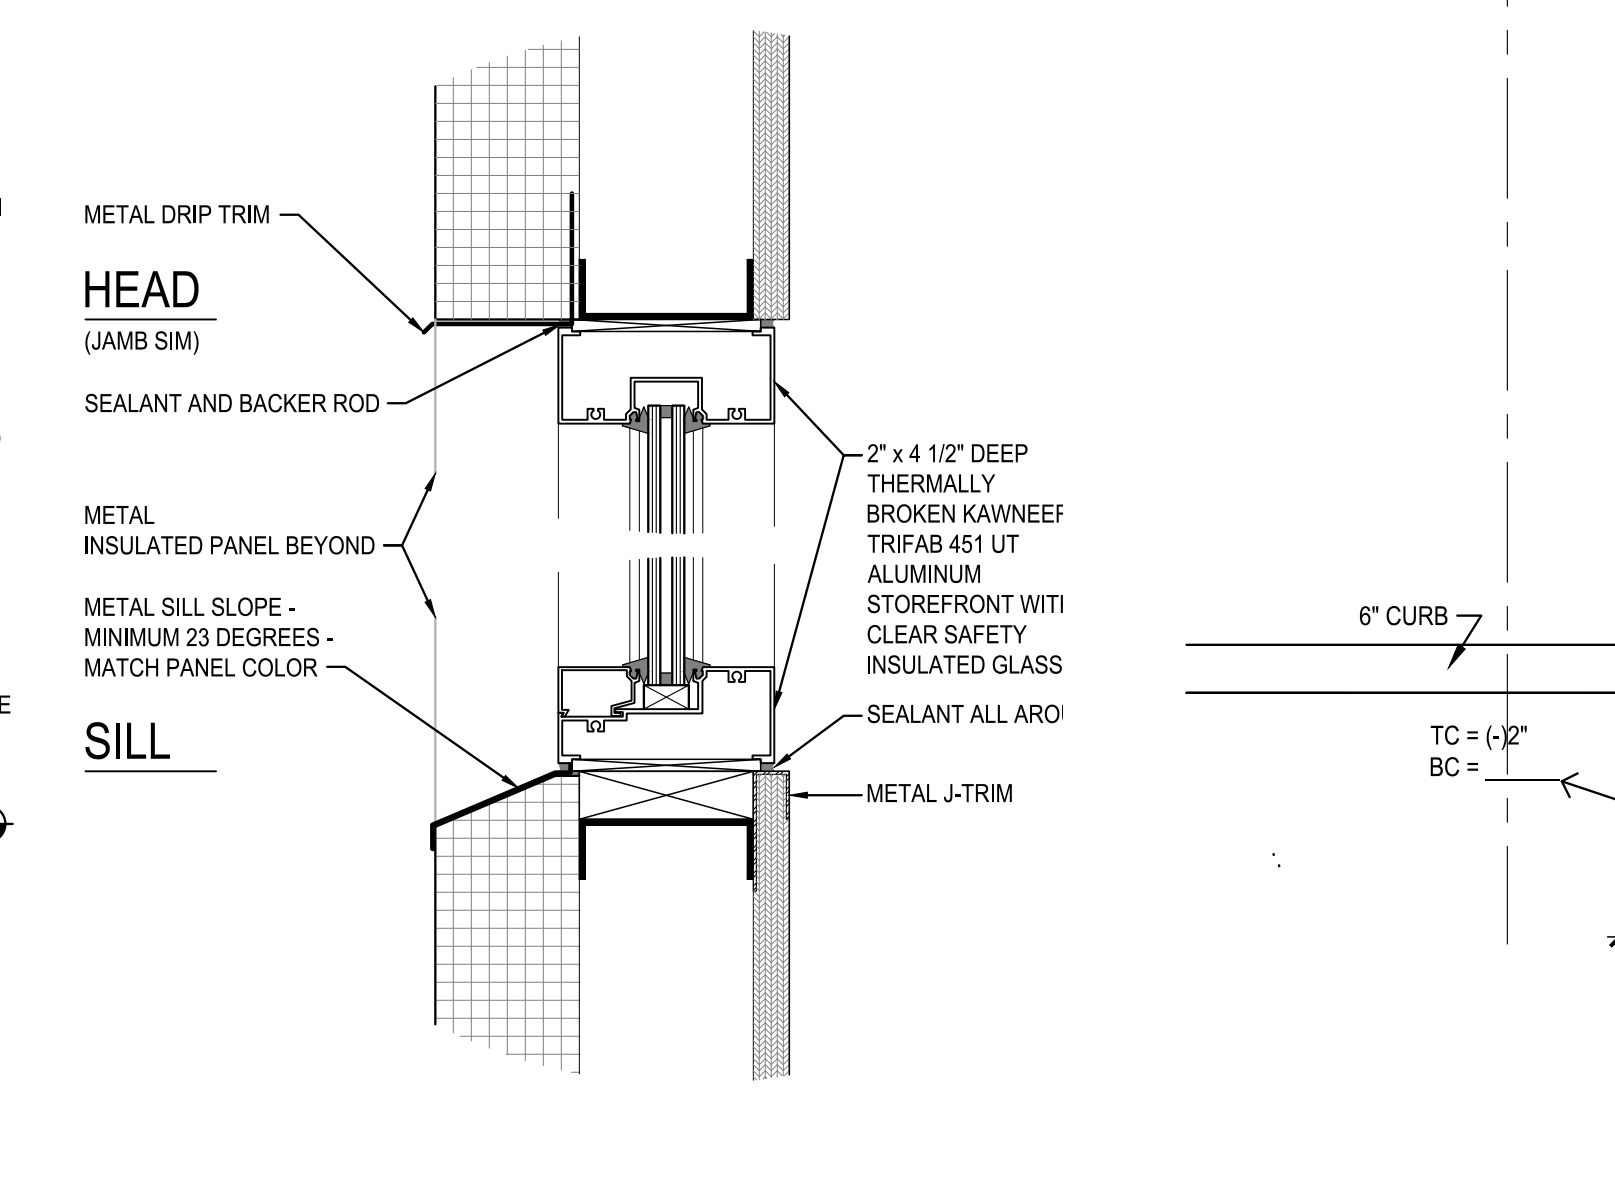


18 WINDOW JAMB
SCALE: 3" = 1'-0" 0122

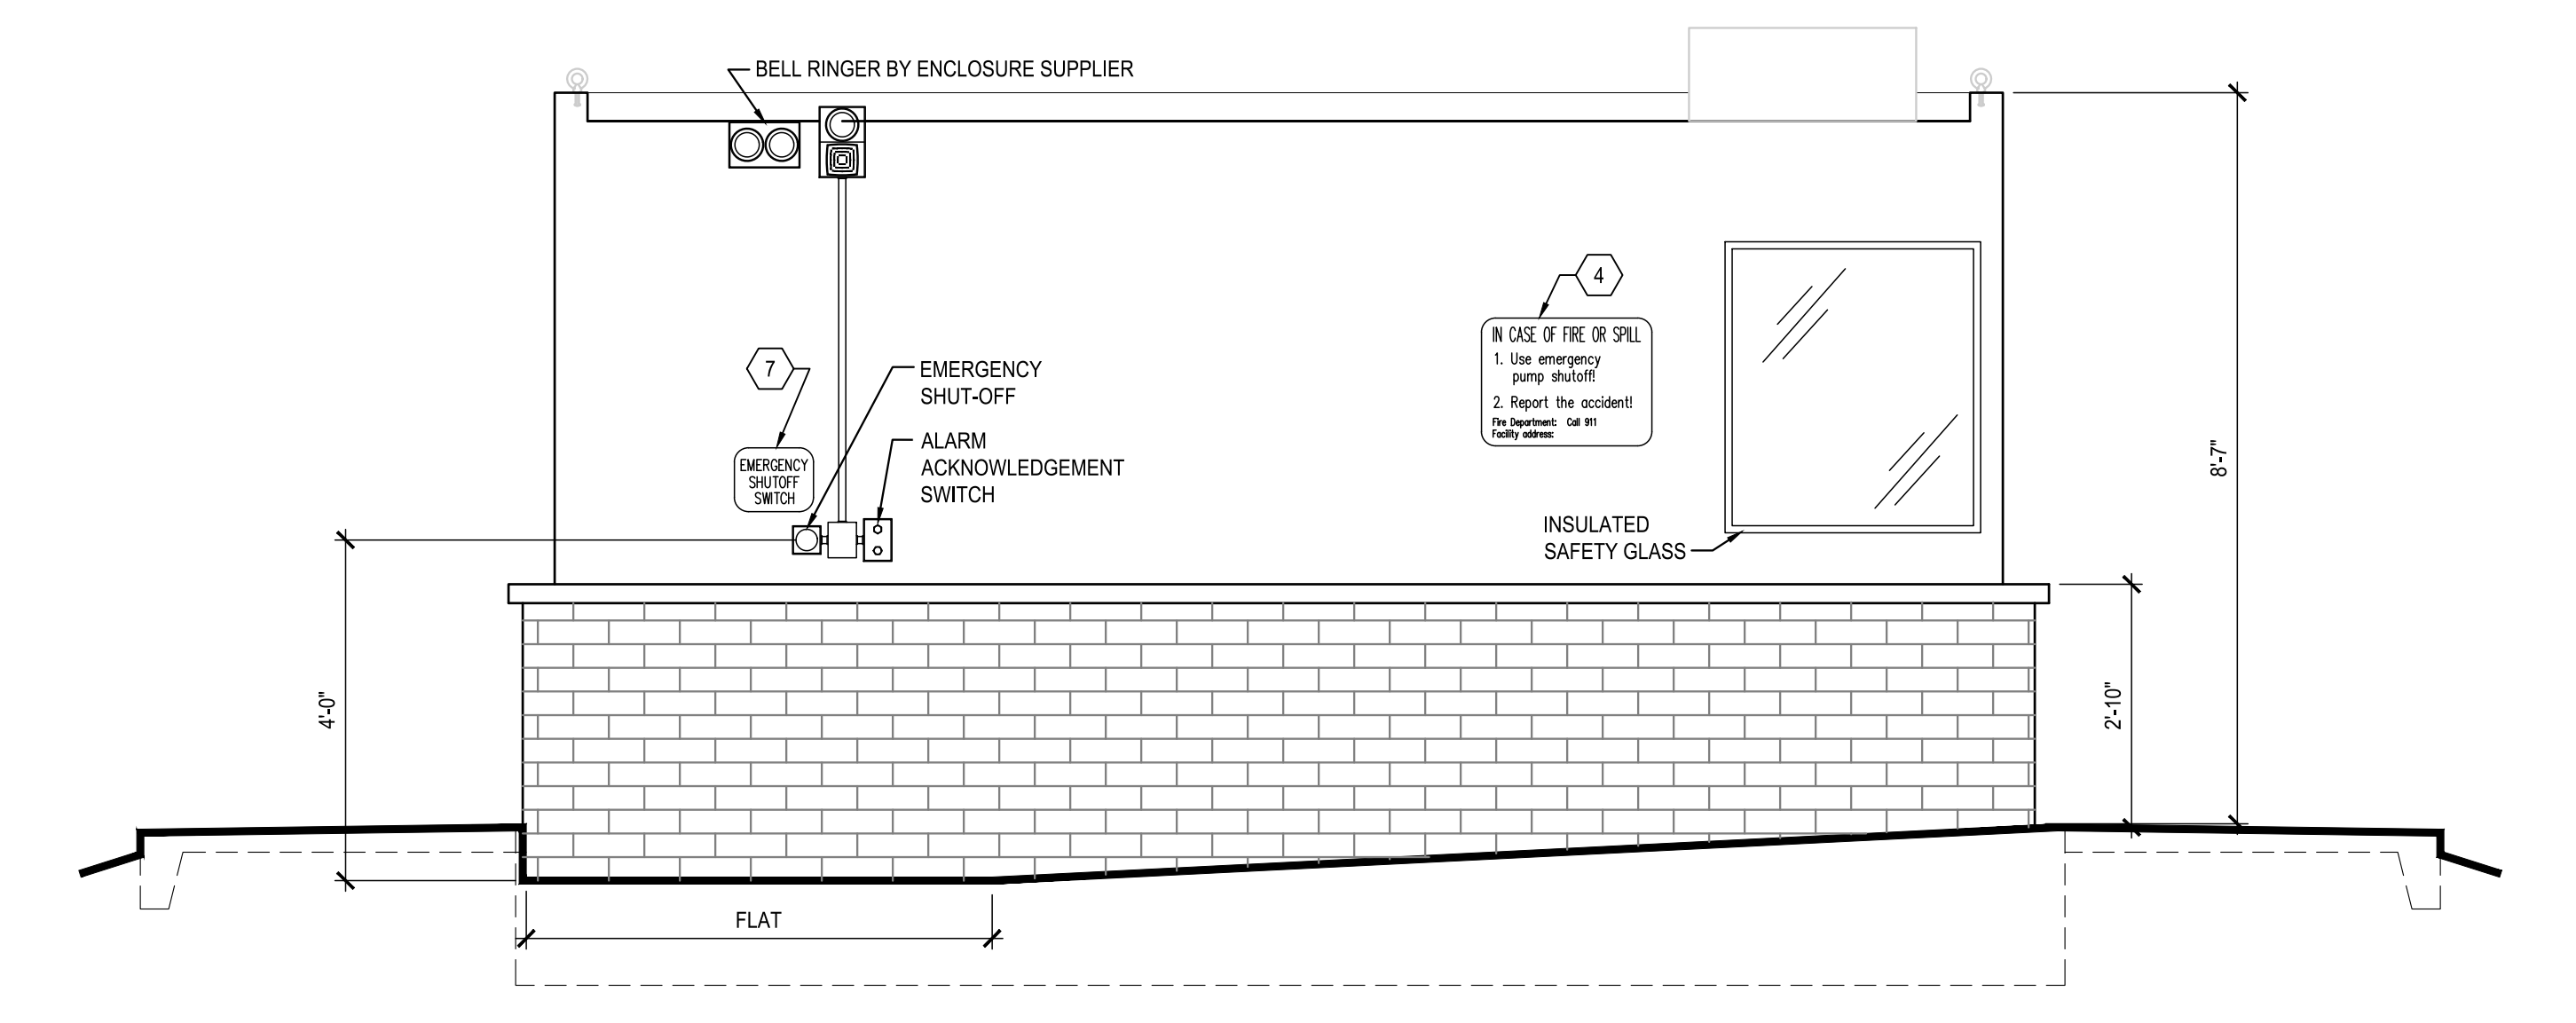

4 SIDE FACING CANOPY
SCALE: 1/2" = 1'-0" 0421

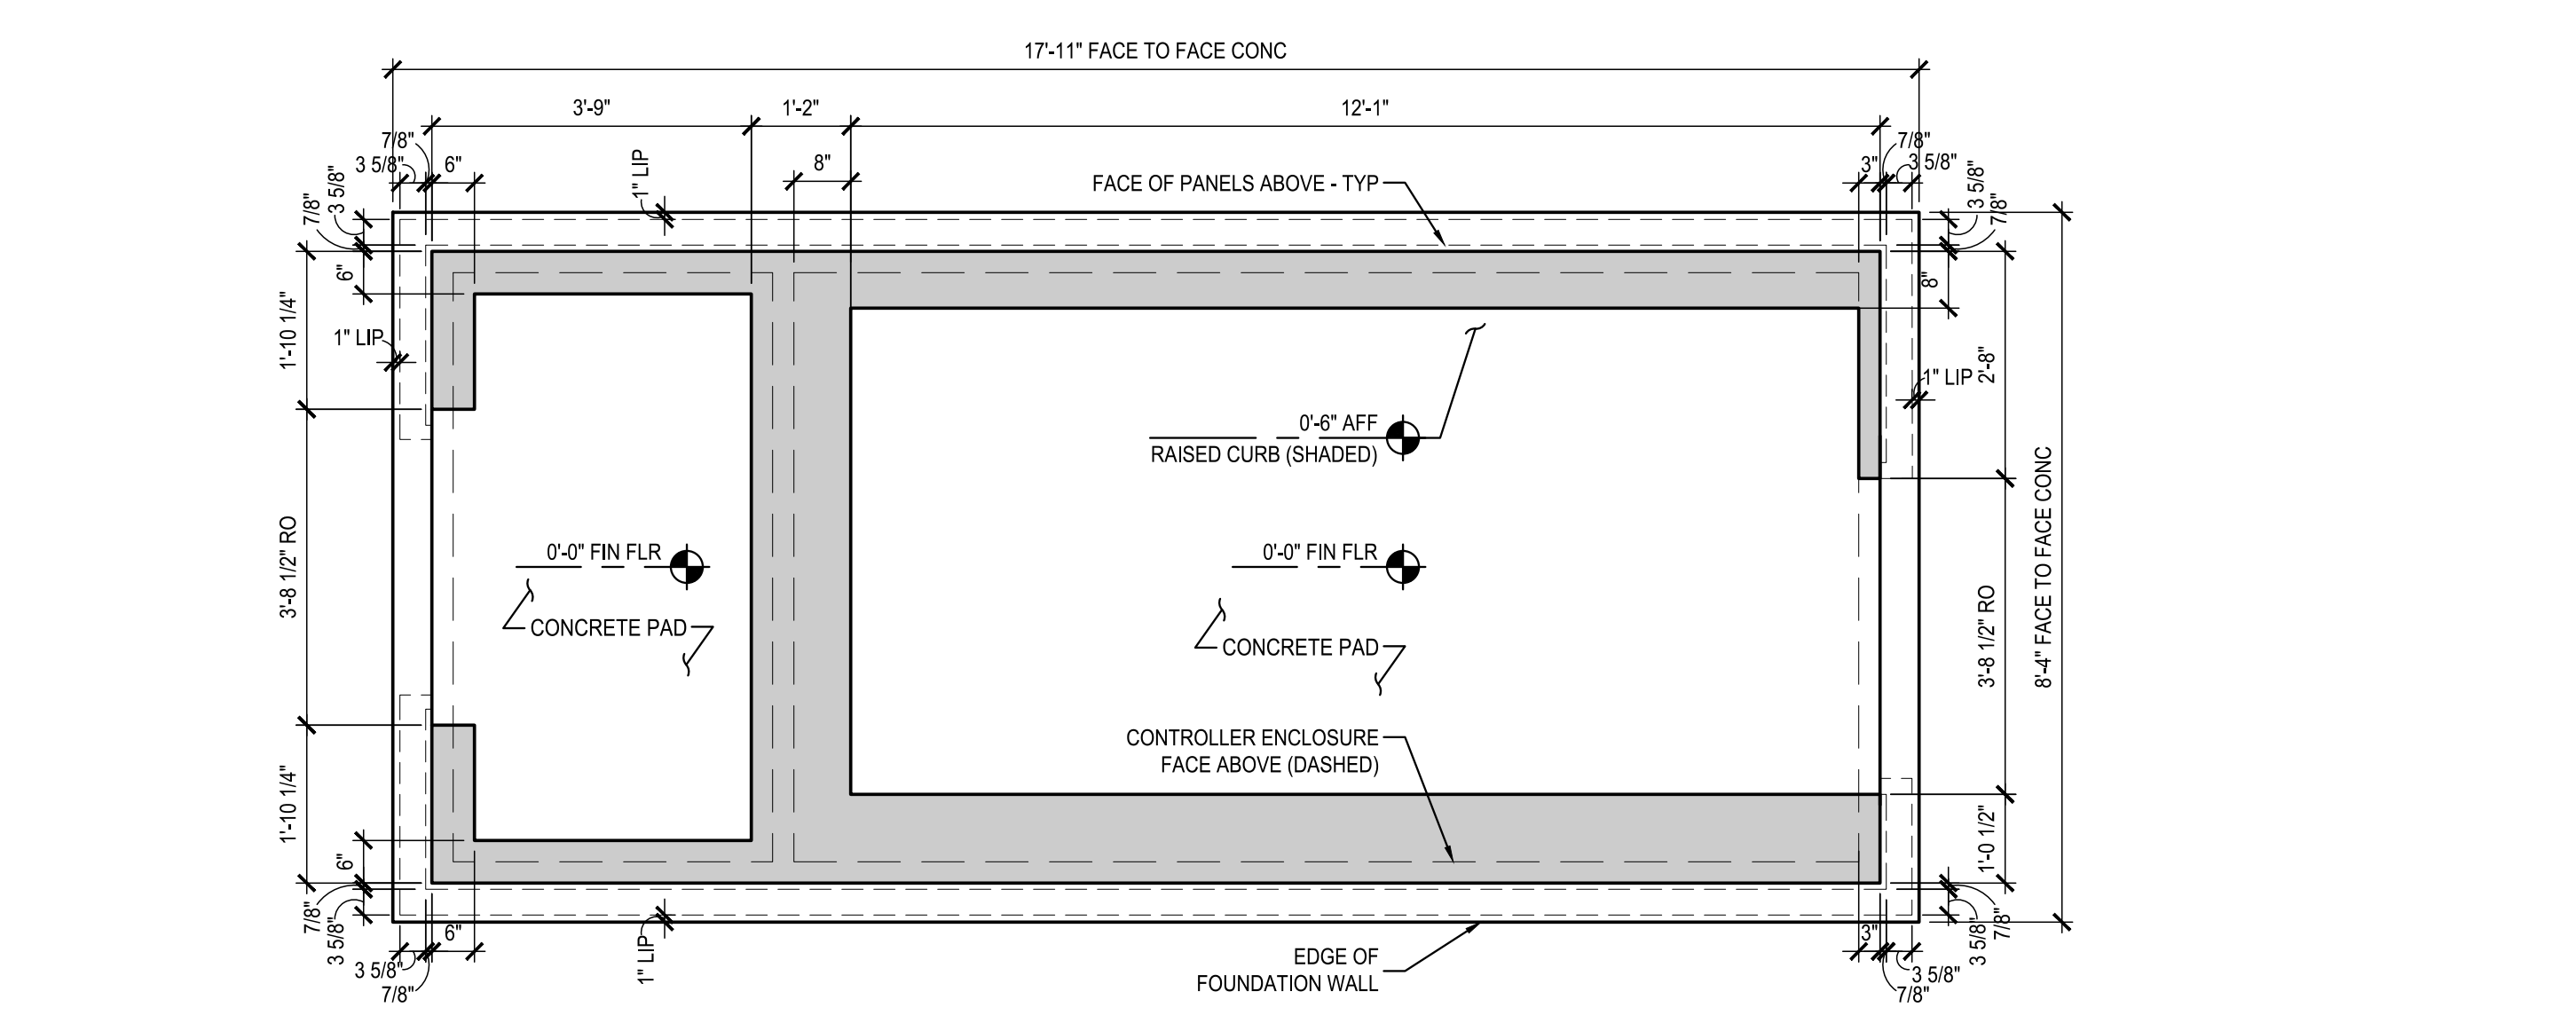

9 FOUNDATION PLAN
SCALE: 1/2" = 1'-0" 1222

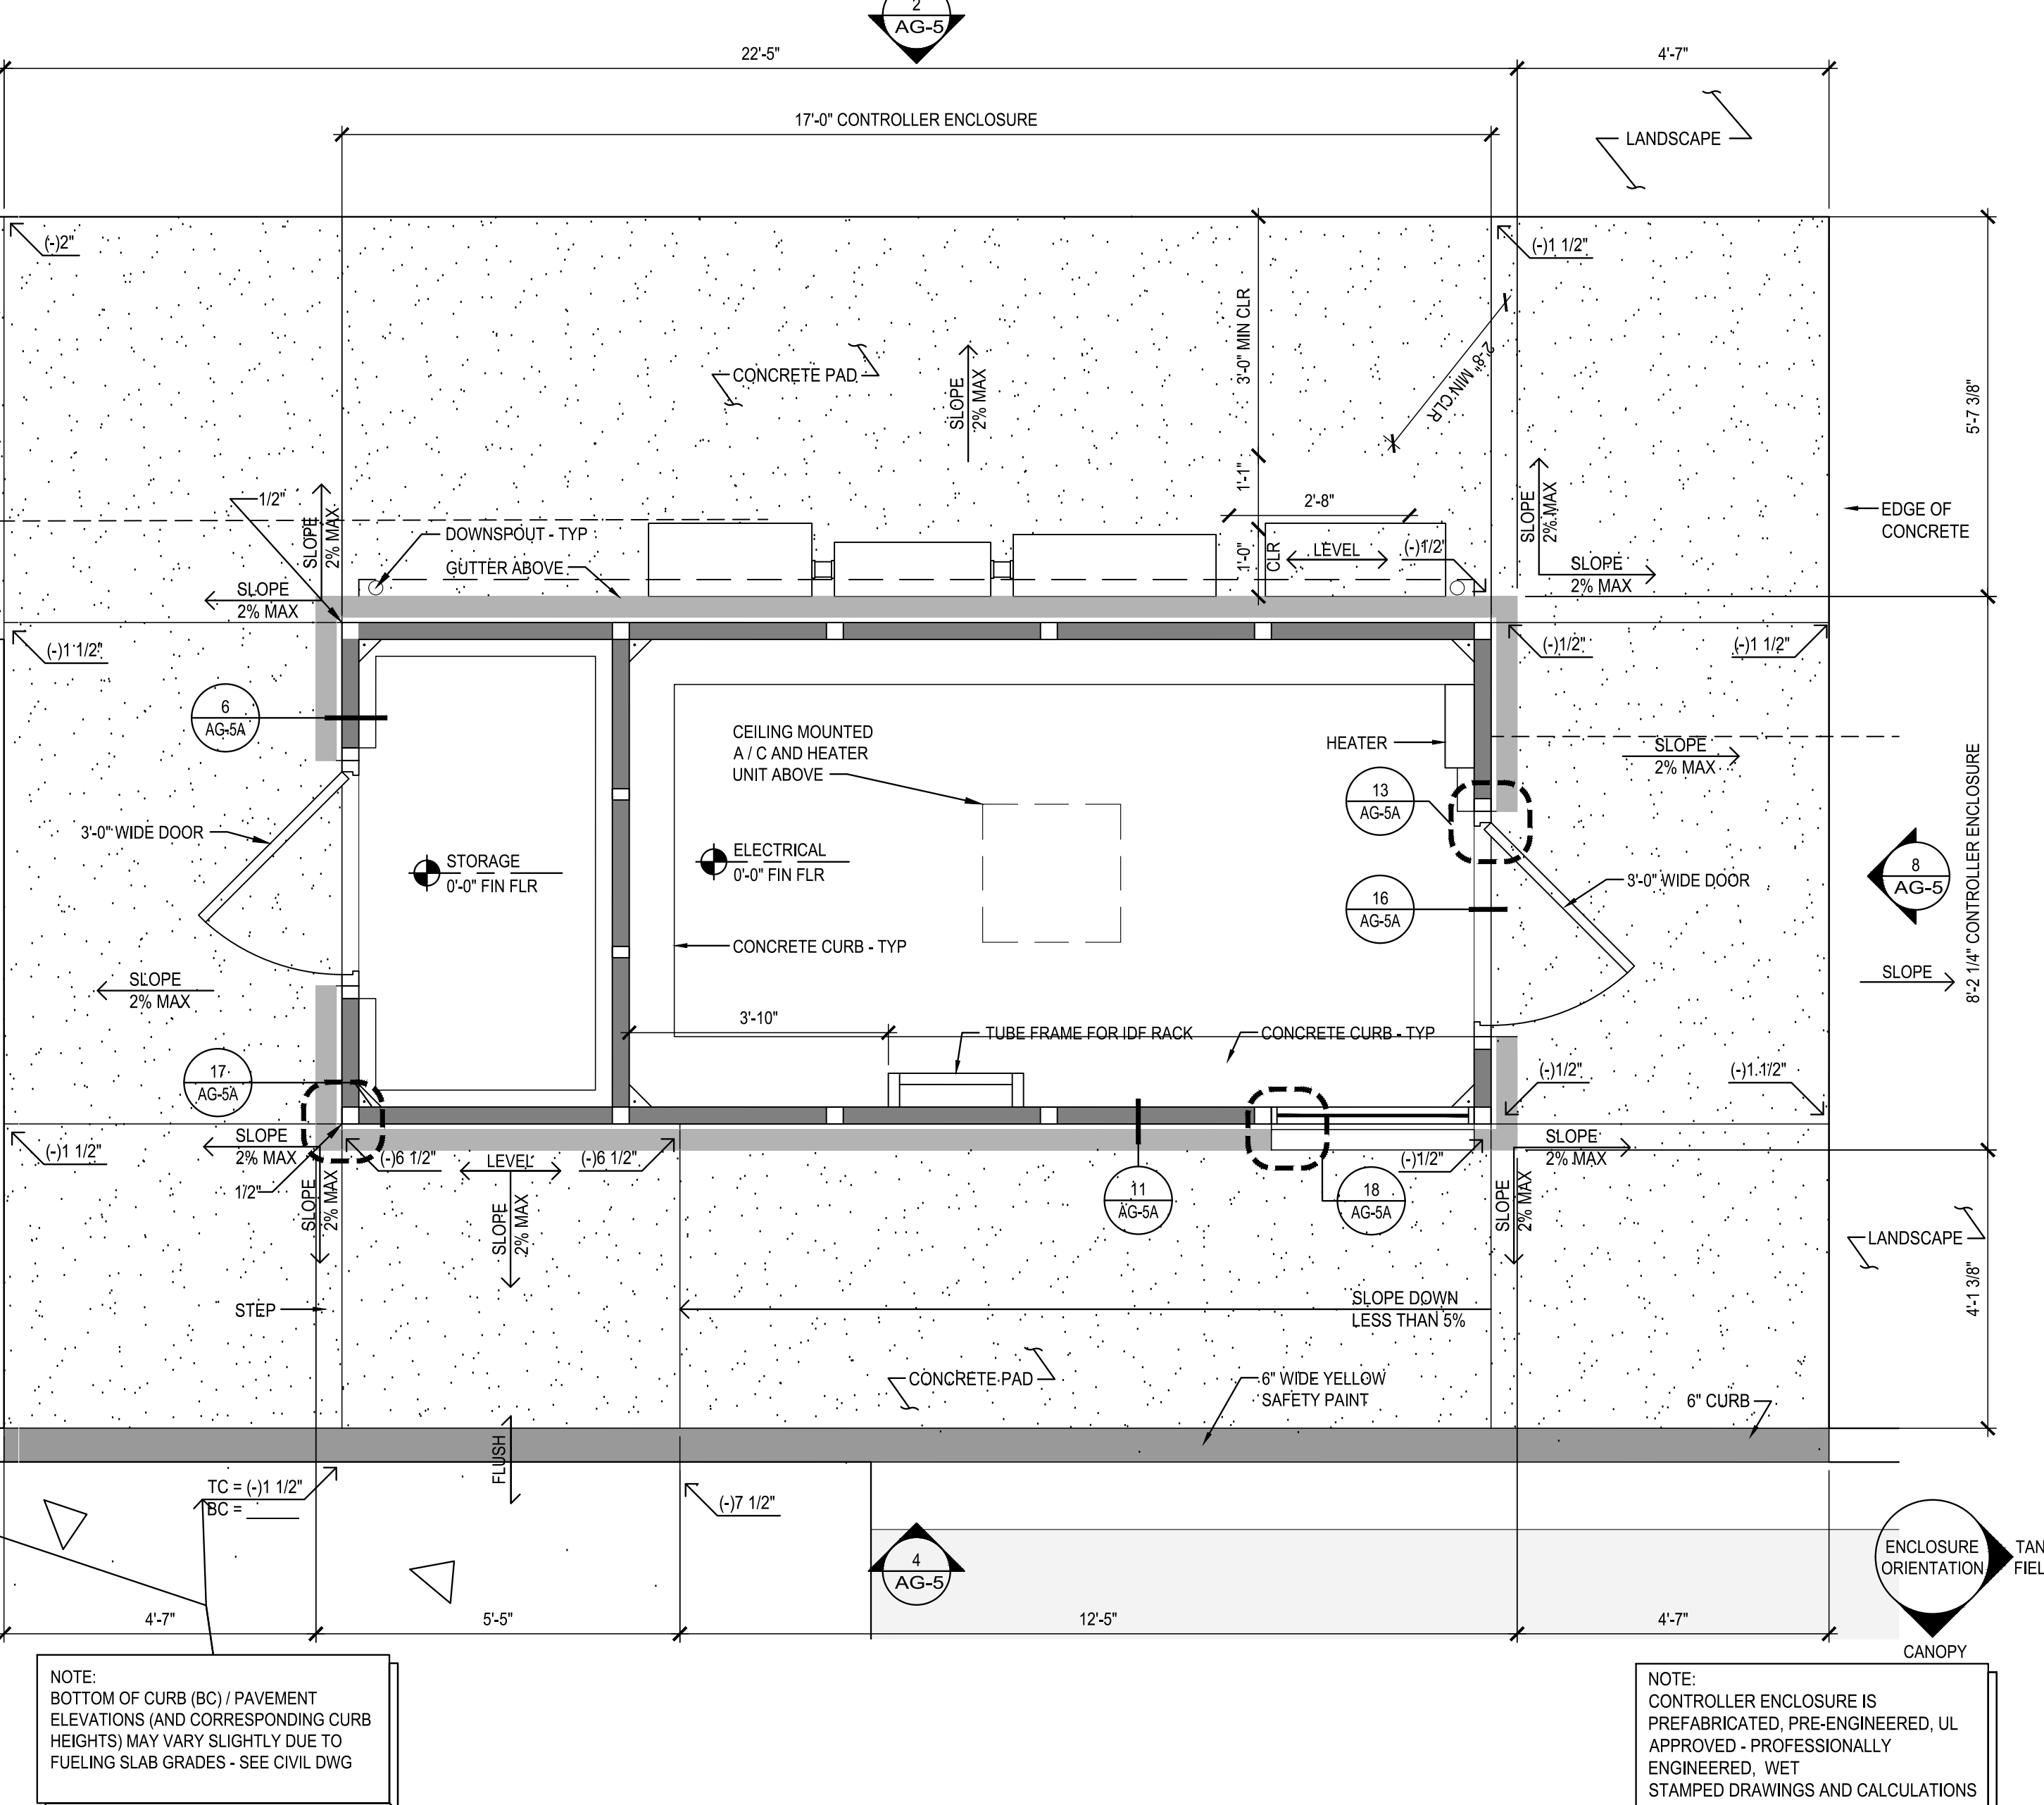

19 STANDARD CONTROLLER ENCLOSURE PLAN
SCALE: 1/2" = 1'-0" 1222

COSTCO
GASOLINE
SE MEMPHIS, TN
#353
3771 HACKS CROSS ROAD
MEMPHIS, TN 38125

COSTCO
WHOLESALE
CORPORATION
730 LAKE DRIVE
ISSAQUAH, WA 98027
T: 425.313.8100
www.costco.com

8444 Westpark Dr, Ste 120
McLean, VA 22102
703.564.8484
MG2.com

MG2

ISSUE FOR
BID

DOUGLAS E. BROOKBANK, ARCHITECT

DATE	DESCRIPTION
02/22/24	PERMIT SET
03/05/24	ISSUE FOR BID

98-4150-19
PM: AGNES VINCENT
DRAWN: AV

CONTROLLER ENCLOSURE PLANS,
ELEVATIONS,
AND DETAILS
AG-5